



---

**PRISCILA CLAUDINO**

EXECUTIVO - SUÍTE CASAL



CLIENTE: **PRISCILA CLAUDINO**

AMBIENTE: **Suíte Casal**

PROJETISTA TÉCNICO: **JOÃO FELIPE SANTOS**

ARQUITETA: **FERNANDA**

**ATENÇÃO:**

DECLARO ESTAR DE ACORDO COM ESTE PROJETO E COM AS MEDIDAS NELE DESCRITAS E CIENTE DE QUE NELE CONSTAM APENAS PEÇAS E MÓDULOS DA EMPRESA, SENDO QUE OS DEMAIS ITENS SÃO MERAMENTE ILUSTRATIVOS (TAIS COMO ELETROS, COLCHÕES, GRANITOS E DECORAÇÕES NO GERAL).

ASS: \_\_\_\_\_

**PRANCHA  
02**

## **CONTRATO**

### **LEIA COM ATENÇÃO**

**1-** CLIENTE ESTÁ RECEBENDO UMA CÓPIA DOS PROJETOS ADQUIRIDOS E ESTÁ DE ACORDO COM AS INFORMAÇÕES APONTADAS SOBRE MODELO, COR, ACABAMENTO, ESTRUTURAS, ACESSÓRIOS E CONDIÇÕES QUE FAZEM PARTE DESTES PROJETOS EXECUTIVOS.

**2-** O MESMO FOI ELABORADO CONSIDERANDO AS MEDIDAS REAIS DESTES AMBIENTES, SE HOUVER ALGUMA ALTERAÇÃO NO PÉ DIREITO OU NAS PAREDES, REFERENTE À INSTALAÇÃO DE MOLDURAS DE GESSO, RODAPÉS, MODIFICAÇÃO EM INSTALAÇÃO DA MODULAÇÃO NO DIA DA MONTAGEM, A EMPRESA NÃO SE RESPONSABILIZA QUANTO A FUTUROS CONTRATEMPOS DEVIDOS ÀS ALTERAÇÕES. CABE AO CLIENTE AVISAR O PROJETISTA ANTES DA MEDIÇÃO FINAL PARA ADEQUAÇÃO DA MODULAÇÃO.

**3-** SE HOUVER GRANITO NOS AMBIENTES, A MEDIÇÃO FINAL SE DARÁ APÓS A CONCLUSÃO DA INSTALAÇÃO DOS MESMOS, OU INSTALAR APÓS A MONTAGEM DOS MÓVEIS.

**4-** SE HOUVER REDUÇÃO OU RECORTES NOS MÓDULOS, O CLIENTE TOMA CIÊNCIA QUE OS AJUSTES SERÃO EXECUTADOS NO LOCAL, QUE DEVE ESTAR LIVRE DE OBJETOS E PESSOAS QUE POSSAM SOFRER DE ALGUMA MANEIRA COM O PÓ DECORRENTE DESSES AJUSTES E QUALQUER OBJETO QUE NÃO POSSA SER RETIRADO DEVE ESTAR DEVIDAMENTE COBERTO. POR NÃO POSSUIR PROFISSIONAIS ESPECIALIZADOS EM INSTALAÇÕES DE ELETROS, INSTALAÇÕES HIDRÁULICAS, A EMPRESA NÃO EFETUARÁ ESSE TIPO DE SERVIÇO. É NECESSÁRIO FORNECER AS PLANTAS DE INSTALAÇÃO ELÉTRICA E HIDRÁULICA DOS AMBIENTES NO DIA DA MONTAGEM, É NECESSÁRIO O ACOMPANHAMENTO DO CLIENTE OU UM RESPONSÁVEL PELA OBRA, MAIOR QUE 18 ANOS PARA TIRAR EVENTUAIS DÚVIDAS DOS MONTADORES REFERENTE AOS LOCAIS ONDE É POSSÍVEL FAZER FURAÇÕES. A ASSINATURA DESSE PROJETO SUBSTITUI QUALQUER PROJETO ANTERIOR.

**5-** O CLIENTE DECLARA ESTAR CIENTE QUE CASO O PROJETO ENVOLVA ELETROS, OS MESMOS DEVERÃO ESTAR NO LOCAL NO DIA DA MONTAGEM PARA ADEQUAÇÃO DOS NICHOS NECESSÁRIOS, E SE NÃO COMPROU OS ELETROS, SE RESPONSABILIZA EM ADQUIRIR OS MESMOS DENTRO DAS MEDIDAS ESPECIFICADAS NESTE PROJETO.

**6-** DECLARO ESTAR DE ACORDO COM ESTE PROJETO E COM AS MEDIDAS NELE DESCRITAS E CIENTE DE QUE NELE CONSTAM APENAS PEÇAS E MÓDULOS DA EMPRESA DUO PLANEJADOS, SENDO QUE OS DEMAIS ITENS SÃO MERAMENTE ILUSTRATIVOS (TAIS COMO ELETROS, COLCHÕES, GRANITOS E DECORAÇÕES EM GERAL).



CLIENTE: **PRISCILA CLAUDINO**

AMBIENTE: **Suíte Casal**

PROJETISTA TÉCNICO: **JOÃO FELIPE SANTOS**

ARQUITETA: **FERNANDA**

**ATENÇÃO:**

DECLARO ESTAR DE ACORDO COM ESTE PROJETO E COM AS MEDIDAS NELE DESCRITAS E CIENTE DE QUE NELE CONSTAM APENAS PEÇAS E MÓDULOS DA EMPRESA, SENDO QUE OS DEMAIS ITENS SÃO MERAMENTE ILUSTRATIVOS (TAIS COMO ELETROS, COLCHÕES, GRANITOS E DECORAÇÕES NO GERAL).

ASS.: \_\_\_\_\_

**PRANCHA  
03**

## PLANTA - ESPECIFICAÇÕES DO PROJETO

### ESPECIFICAÇÕES DO PROJETO

#### CORES E ACABAMENTOS:

Caixa Módulos (Interno): **Branco, Freijo Puro**

Portas e Frentes: **Nude, Branco, Freijo Puro**

Tamponamentos: **Nude, Freijo Puro, Branco**

Painéis e Tampos: **Freijo Puro, Branco, Nude**

Puxadores: **Champagne**

Portas de Vidro:

#### FERRAGENS E ACESSÓRIOS:

Dobradiças:

**Dobradiça Reta c/ Amortecedor, Dobradiça Curva c/ Amortecedor**

Corrediças: **Gaveta Corrediça Telescópica**

Puxadores:

**Puxador Linear (15, 18 e 20mm) Pino Champagne - 200mm**

Ferragens especiais: **Cabideiro Tubo s/ Reforço**

#### ESPESSURAS:


Caixa Módulos (Interno): **18mm (fundo 6mm)**

Prateleiras internas: **18mm**

Portas e Frentes: **18mm**

Tamponamentos: **15mm e 18mm e 25mm**

Painéis e Tampos e perfil: **15mm e 18mm e 25mm**

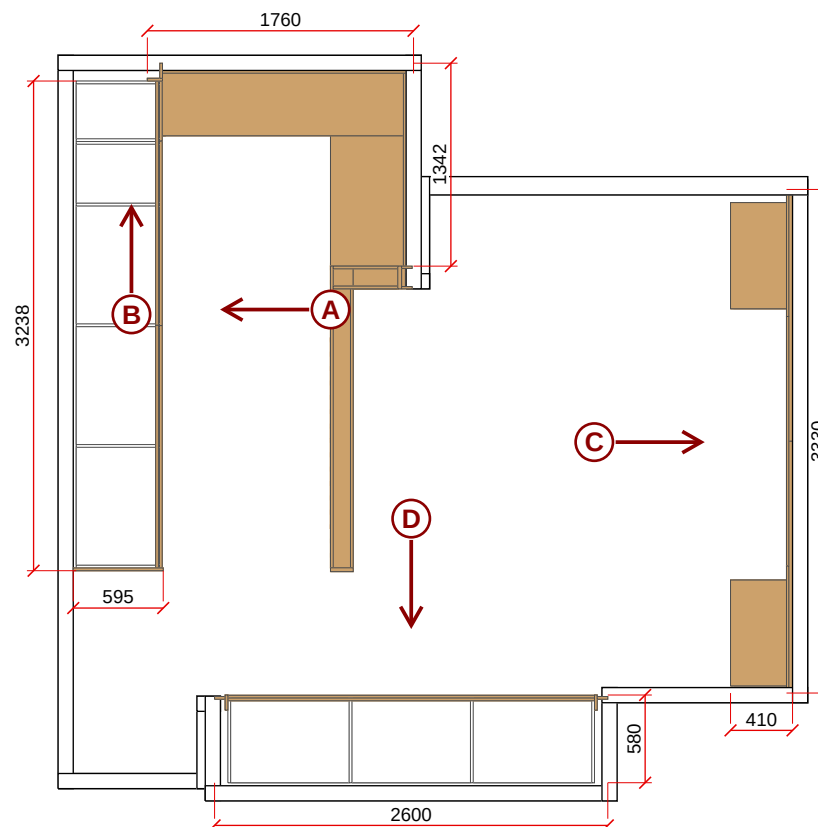

PLANTA BAIXA - ESC. 1:50



CLIENTE: **PRISCILA CLAUDINO**

AMBIENTE: **Suíte Casal**

PROJETISTA TÉCNICO: **JOÃO FELIPE SANTOS**

ARQUITETA: **FERNANDA**

**ATENÇÃO:**


DECLARO ESTAR DE ACORDO COM ESTE PROJETO E COM AS MEDIDAS NELE DESCRITAS E CIENTE DE QUE NELE CONSTAM APENAS PEÇAS E MÓDULOS DA EMPRESA, SENDO QUE OS DEMAIS ITENS SÃO MERAMENTE ILUSTRATIVOS (TAIS COMO ELETROS, COLCHÕES, GRANITOS E DECORAÇÕES NO GERAL).

ASS.: \_\_\_\_\_


**PRANCHA  
04**

**VISÃO GERAL DOS MÓVEIS**

**VISTA A**

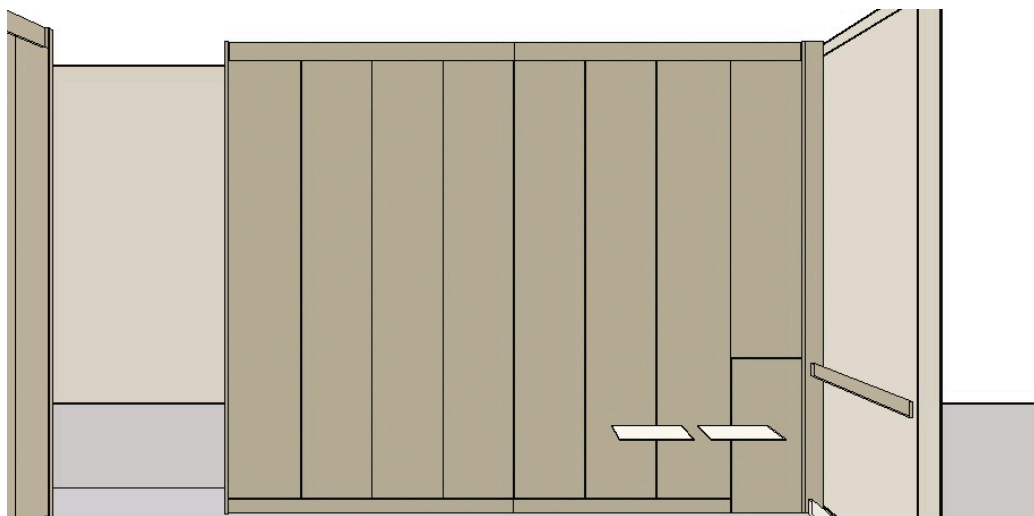


**VISTA B**

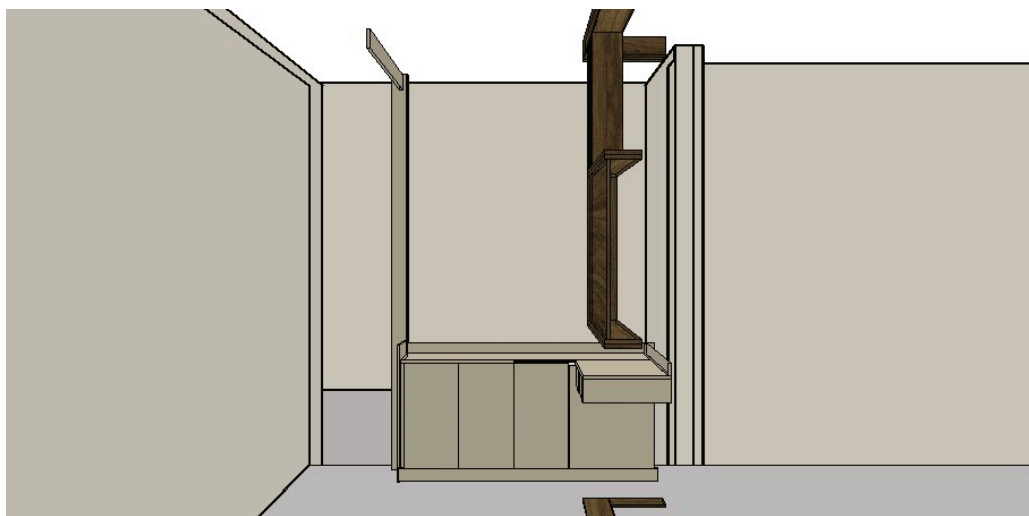

**VISTA C**



**VISTA D**

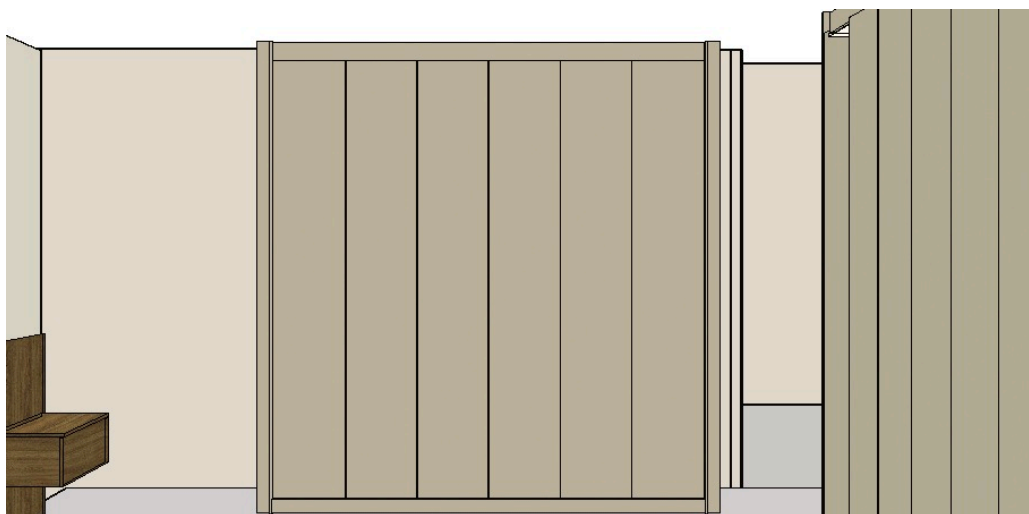



CLIENTE: **PRISCILA CLAUDINO**

AMBIENTE: **Suíte Casal**

PROJETISTA TÉCNICO: **JOÃO FELIPE SANTOS**

ARQUITETA: **FERNANDA**

**ATENÇÃO:**


DECLARO ESTAR DE ACORDO COM ESTE PROJETO E COM AS MEDIDAS NELE DESCRITAS E CIENTE DE QUE NELE CONSTAM APENAS PEÇAS E MÓDULOS DA EMPRESA, SENDO QUE OS DEMAIS ITENS SÃO MERAMENTE ILUSTRATIVOS (TAIS COMO ELETROS, COLCHÕES, GRANITOS E DECORAÇÕES NO GERAL).

ASS.: \_\_\_\_\_

**PRANCHA  
05**

## MÓDULOS E PAINÉIS - VISTA A

| Item | Descrição                           | Dimensão      |
|------|-------------------------------------|---------------|
| 1    | Armário c/ Portas de Giro c/ Rodapé | 2820x2540x550 |
| 2    | Armário c/ Portas de Giro c/ Rodapé | 400x2540x550  |
| 3    | Painel Nude MDP                     | 868x18x396    |
| 4    | Tamponamento Inferior               | 1217x18x80    |
| 5    | Tamponamento Inferior               | 1603x18x80    |
| 6    | Tamponamento Inferior               | 2645x18x595   |
| 7    | Tamponamento Inferior               | 1605x18x100   |
| 8    | Tamponamento Inferior               | 1615x18x100   |

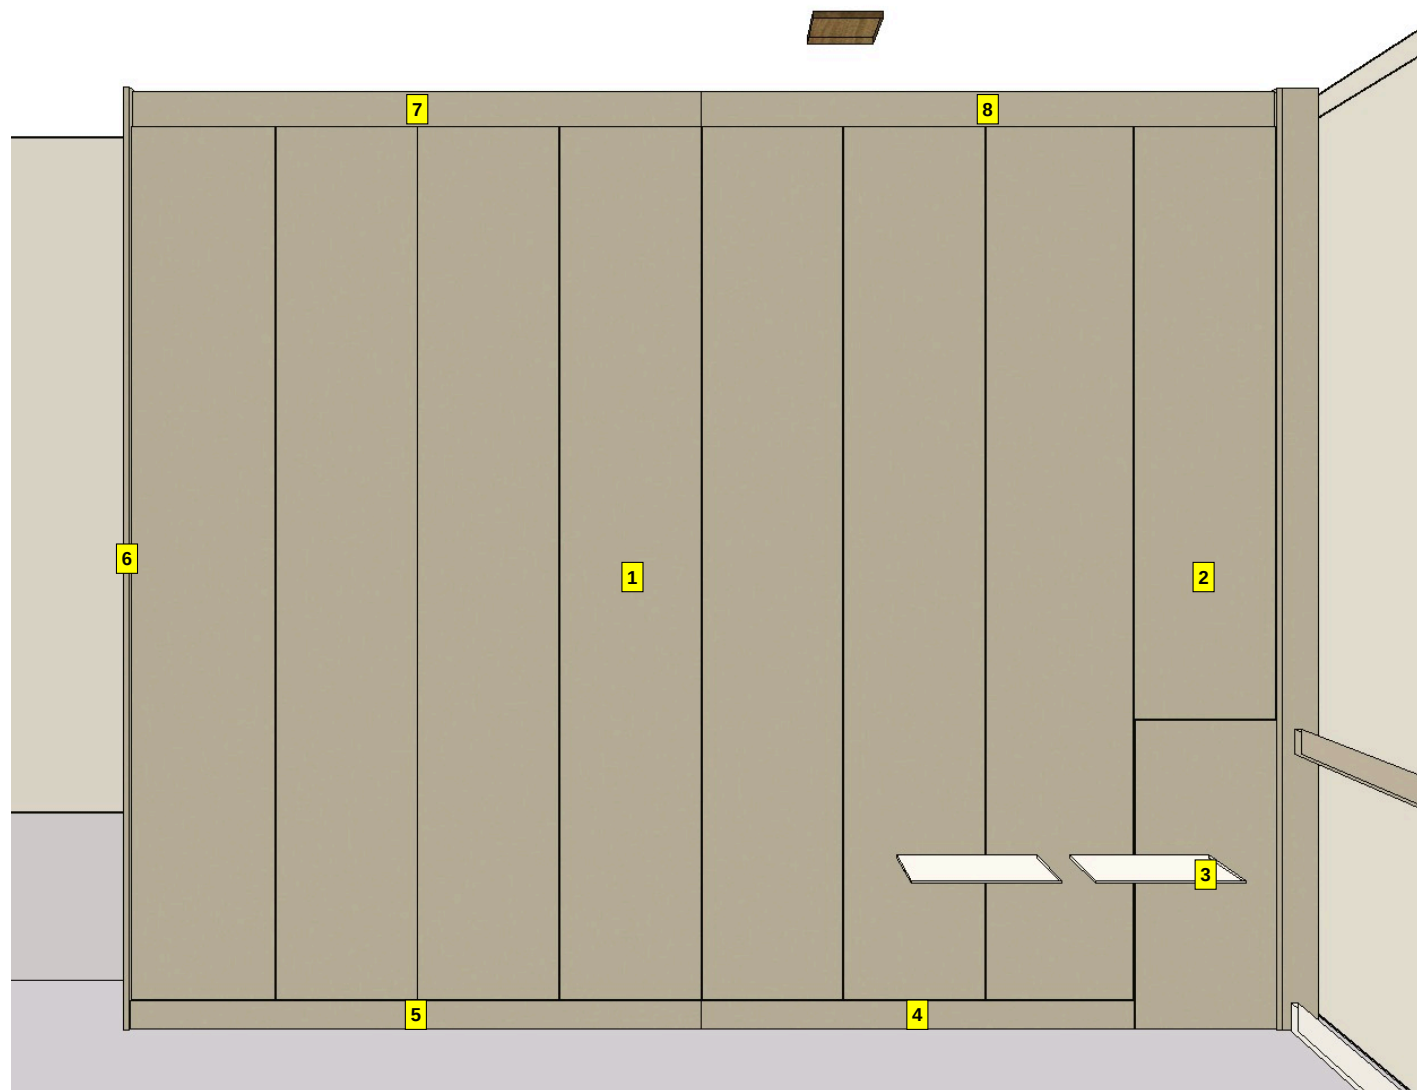



CLIENTE: **PRISCILA CLAUDINO**

AMBIENTE: **Suíte Casal**

PROJETISTA TÉCNICO: **JOÃO FELIPE SANTOS**

ARQUITETA: **FERNANDA**

**ATENÇÃO:**

DECLARO ESTAR DE ACORDO COM ESTE PROJETO E COM AS MEDIDAS NELE DESCRITAS E CIENTE DE QUE NELE CONSTAM APENAS PEÇAS E MÓDULOS DA EMPRESA, SENDO QUE OS DEMAIS ITENS SÃO MERAMENTE ILUSTRATIVOS (TAIS COMO ELETROS, COLCHÕES, GRANITOS E DECORAÇÕES NO GERAL).


ASS.: \_\_\_\_\_

**PRANCHA  
06**



## MÓDULOS E PAINÉIS - VISTA B

| Item | Descrição             | Dimensão     |
|------|-----------------------|--------------|
| 1    | Balcão Inferior       | 1560x675x390 |
| 2    | Gaveta                | 820x135x480  |
| 3    | Painel Nude MDP       | 135x18x70    |
| 4    | Painel Nude MDP       | 670x18x540   |
| 5    | Painel Nude MDP       | 1660x18x70   |
| 6    | Painel Nude MDP       | 1660x18x432  |
| 7    | Painel Nude MDP       | 1276x18x70   |
| 8    | Painel Nude MDP       | 862x18x500   |
| 9    | Tamponamento Inferior | 2645x18x100  |
| 10   | Tamponamento Inferior | 1660x18x80   |
| 11   | Tamponamento Inferior | 755x18x100   |
| 12   | Tamponamento Inferior | 341x18x80    |
| 13   | Tamponamento Inferior | 1550x18x80   |
| 14   | Tamponamento Inferior | 135x18x500   |

### BASE DE APOIO · PEÇAS ENCOBERTAS

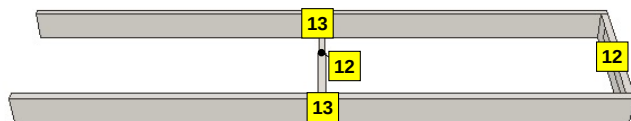

### POSIÇÃO NO MÓVEL

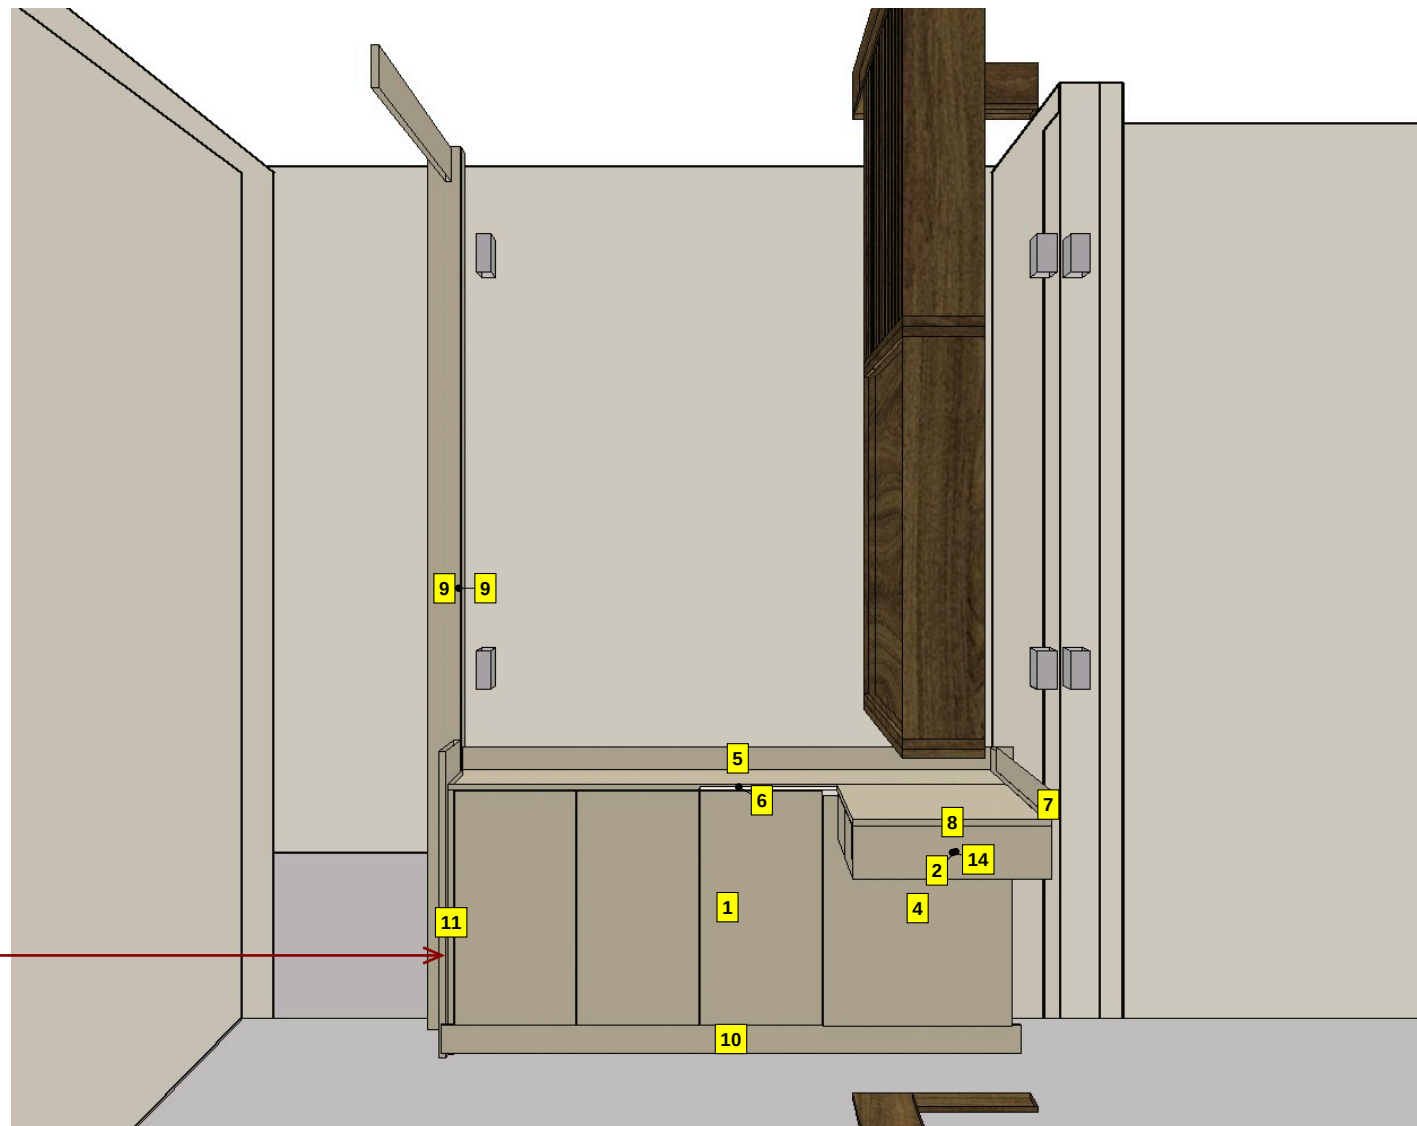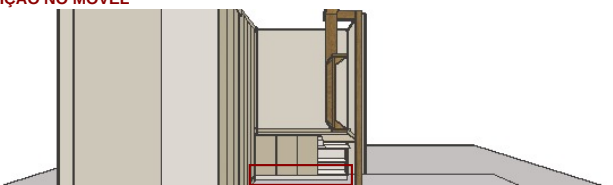



CLIENTE: **PRISCILA CLAUDINO**

AMBIENTE: **Suíte Casal**

PROJETISTA TÉCNICO: **JOÃO FELIPE SANTOS**

ARQUITETA: **FERNANDA**

**ATENÇÃO:**

DECLARO ESTAR DE ACORDO COM ESTE PROJETO E COM AS MEDIDAS NELE DESCRITAS E CIENTE DE QUE NELE CONSTAM APENAS PEÇAS E MÓDULOS DA EMPRESA, SENDO QUE OS DEMAIS ITENS SÃO MERAMENTE ILUSTRATIVOS (TAIS COMO ELETROS, COLCHÕES, GRANITOS E DECORAÇÕES NO GERAL).

ASS: \_\_\_\_\_



**PRANCHA  
07**

**PEÇA ESCONDIDA · Painei Nude MDP · VISTA B**

**PEÇA ESCONDIDA · Painei Nude MDP**



**POSIÇÃO NO MÓVEL**

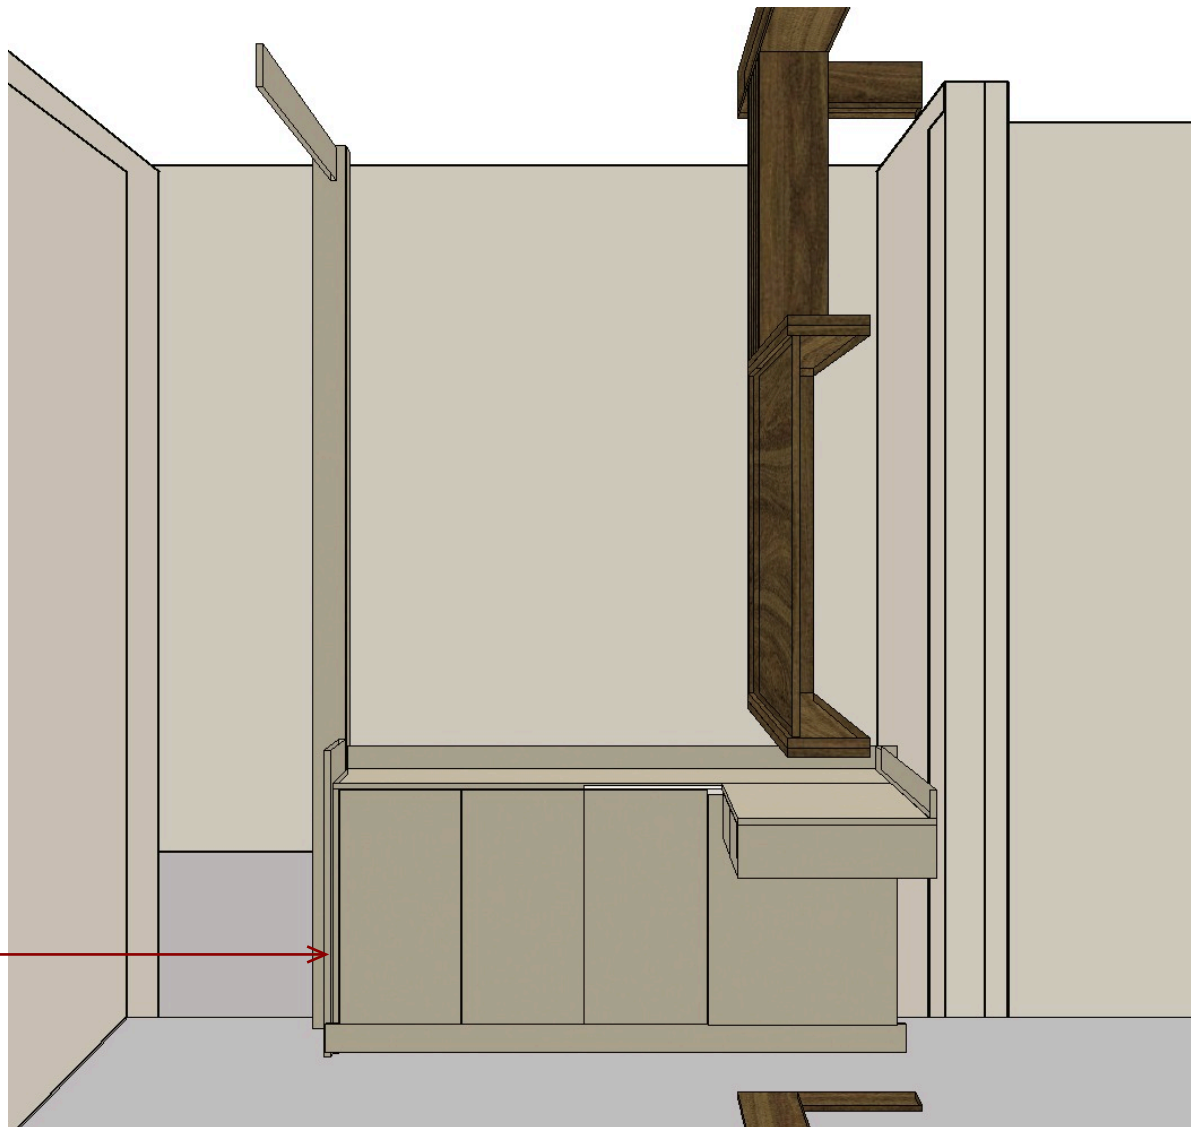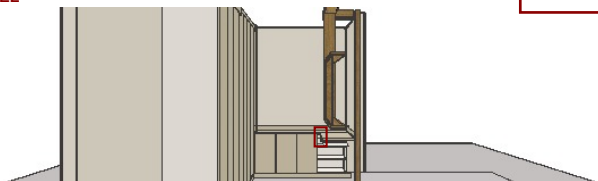





CLIENTE: **PRISCILA CLAUDINO**

AMBIENTE: **Suíte Casal**

PROJETISTA TÉCNICO: **JOÃO FELIPE SANTOS**

ARQUITETA: **FERNANDA**

**ATENÇÃO:**

DECLARO ESTAR DE ACORDO COM ESTE PROJETO E COM AS MEDIDAS NELE DESCRITAS E CIENTE DE QUE NELE CONSTAM APENAS PEÇAS E MÓDULOS DA EMPRESA, SENDO QUE OS DEMAIS ITENS SÃO MERAMENTE ILUSTRATIVOS (TAIS COMO ELETROS, COLCHÕES, GRANITOS E DECORAÇÕES NO GERAL).

ASS.: \_\_\_\_\_

**PRANCHA  
08**



## MÓDULOS E PAINÉIS - VISTA C

| Item | Descrição              | Dimensão     |
|------|------------------------|--------------|
| 1    | Balcão 1 Gaveta        | 700x250x350  |
| 2    | Painel Branco MDF      | 810x25x80    |
| 3    | Painel Branco MDF      | 810x25x100   |
| 4    | Painel Branco MDF      | 1629x25x80   |
| 5    | Painel Freijo Puro MDF | 1010x15x840  |
| 6    | Painel Freijo Puro MDF | 1010x15x1650 |
| 7    | Tamponamento Inferior  | 700x18x370   |
| 8    | Tamponamento Inferior  | 702x18x370   |

**PEÇA ESCONDIDA - Painel Branco MDF**



**POSIÇÃO NO MÓVEL**

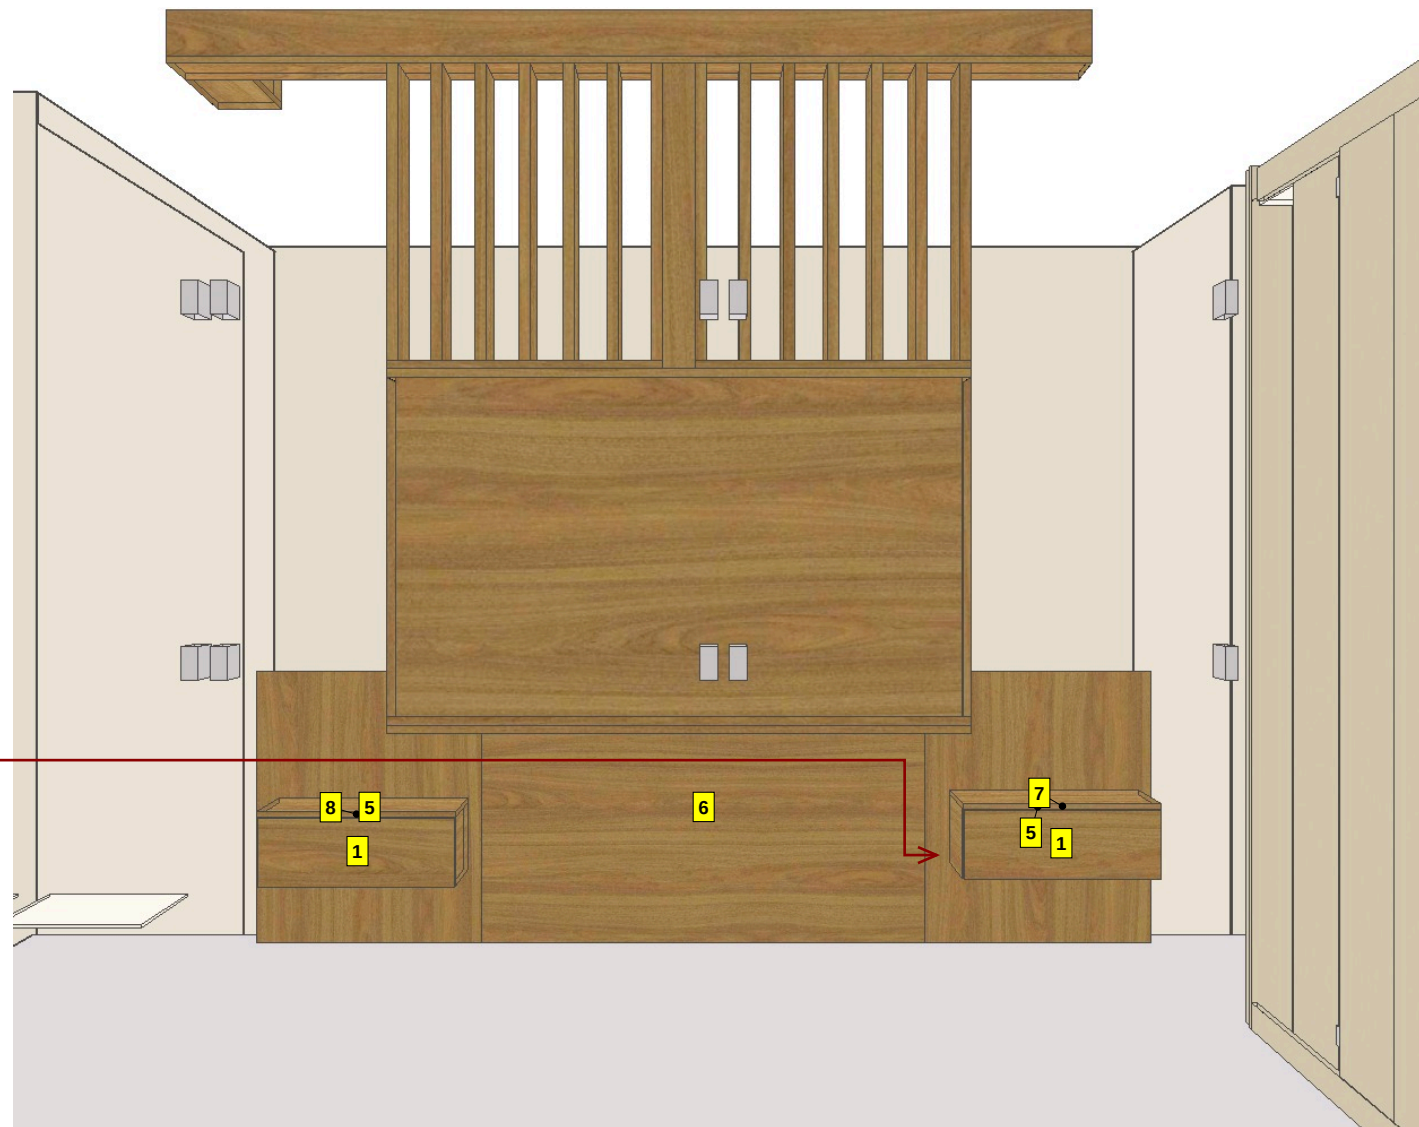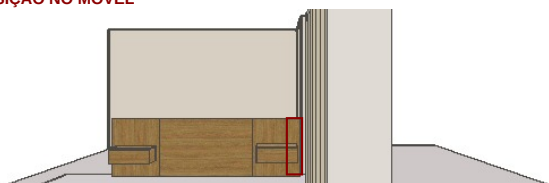





CLIENTE: **PRISCILA CLAUDINO**

AMBIENTE: **Suíte Casal**

PROJETISTA TÉCNICO: **JOÃO FELIPE SANTOS**

ARQUITETA: **FERNANDA**

**ATENÇÃO:**


DECLARO ESTAR DE ACORDO COM ESTE PROJETO E COM AS MEDIDAS NELE DESCRITAS E CIENTE DE QUE NELE CONSTAM APENAS PEÇAS E MÓDULOS DA EMPRESA, SENDO QUE OS DE MAIS ITENS SÃO MERAMENTE ILUSTRATIVOS (TAIS COMO ELETROS, COLCHÕES, GRANITOS E DECORAÇÕES NO GERAL).

ASS: \_\_\_\_\_


**PRANCHA  
09**

**PEÇA ESCONDIDA · Painei Branco MDF · VISTA C**

**PEÇA ESCONDIDA · Painei Branco MDF**

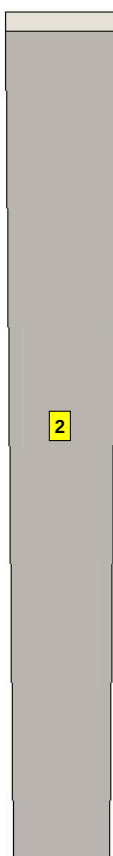

**POSIÇÃO NO MÓVEL**

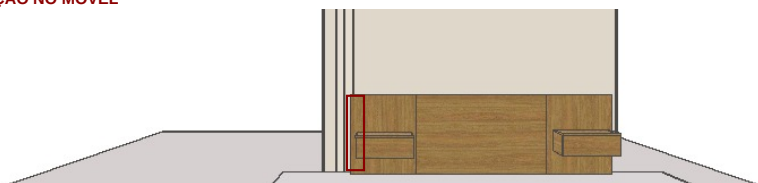



CLIENTE: **PRISCILA CLAUDINO**

AMBIENTE: **Suíte Casal**

PROJETISTA TÉCNICO: **JOÃO FELIPE SANTOS**

ARQUITETA: **FERNANDA**

**ATENÇÃO:**


DECLARO ESTAR DE ACORDO COM ESTE PROJETO E COM AS MEDIDAS NELE DESCRITAS E CIENTE DE QUE NELE CONSTAM APENAS PEÇAS E MÓDULOS DA EMPRESA, SENDO QUE OS DEMAIS ITENS SÃO MERAMENTE ILUSTRATIVOS (TAIS COMO ELETROS, COLCHÕES, GRANITOS E DECORAÇÕES NO GERAL).

ASS: \_\_\_\_\_


**PRANCHA  
10**

**PEÇA ESCONDIDA · Painel Branco MDF · VISTA C**

**PEÇA ESCONDIDA · Painel Branco MDF**

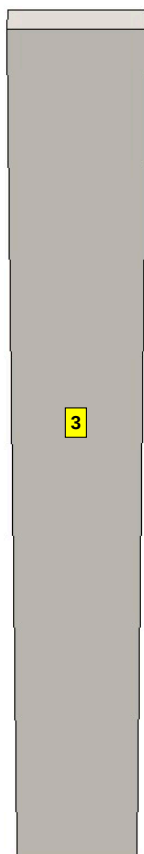

**POSIÇÃO NO MÓVEL**

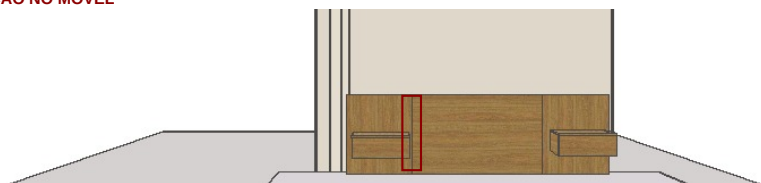



CLIENTE: **PRISCILA CLAUDINO**

AMBIENTE: **Suíte Casal**

PROJETISTA TÉCNICO: **JOÃO FELIPE SANTOS**

ARQUITETA: **FERNANDA**

**ATENÇÃO:**


DECLARO ESTAR DE ACORDO COM ESTE PROJETO E COM AS MEDIDAS NELE DESCRITAS E CIENTE DE QUE NELE CONSTAM APENAS PEÇAS E MÓDULOS DA EMPRESA, SENDO QUE OS DEMAIS ITENS SÃO MERAMENTE ILUSTRATIVOS (TAIS COMO ELETROS, COLCHÕES, GRANITOS E DECORAÇÕES NO GERAL).

ASS: \_\_\_\_\_



# PRANCHA 11

## PEÇA ESCONDIDA · Painel Branco MDF · VISTA C

PEÇA ESCONDIDA · Painel Branco MDF

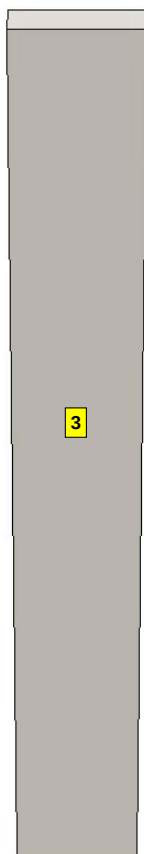

POSIÇÃO NO MÓVEL

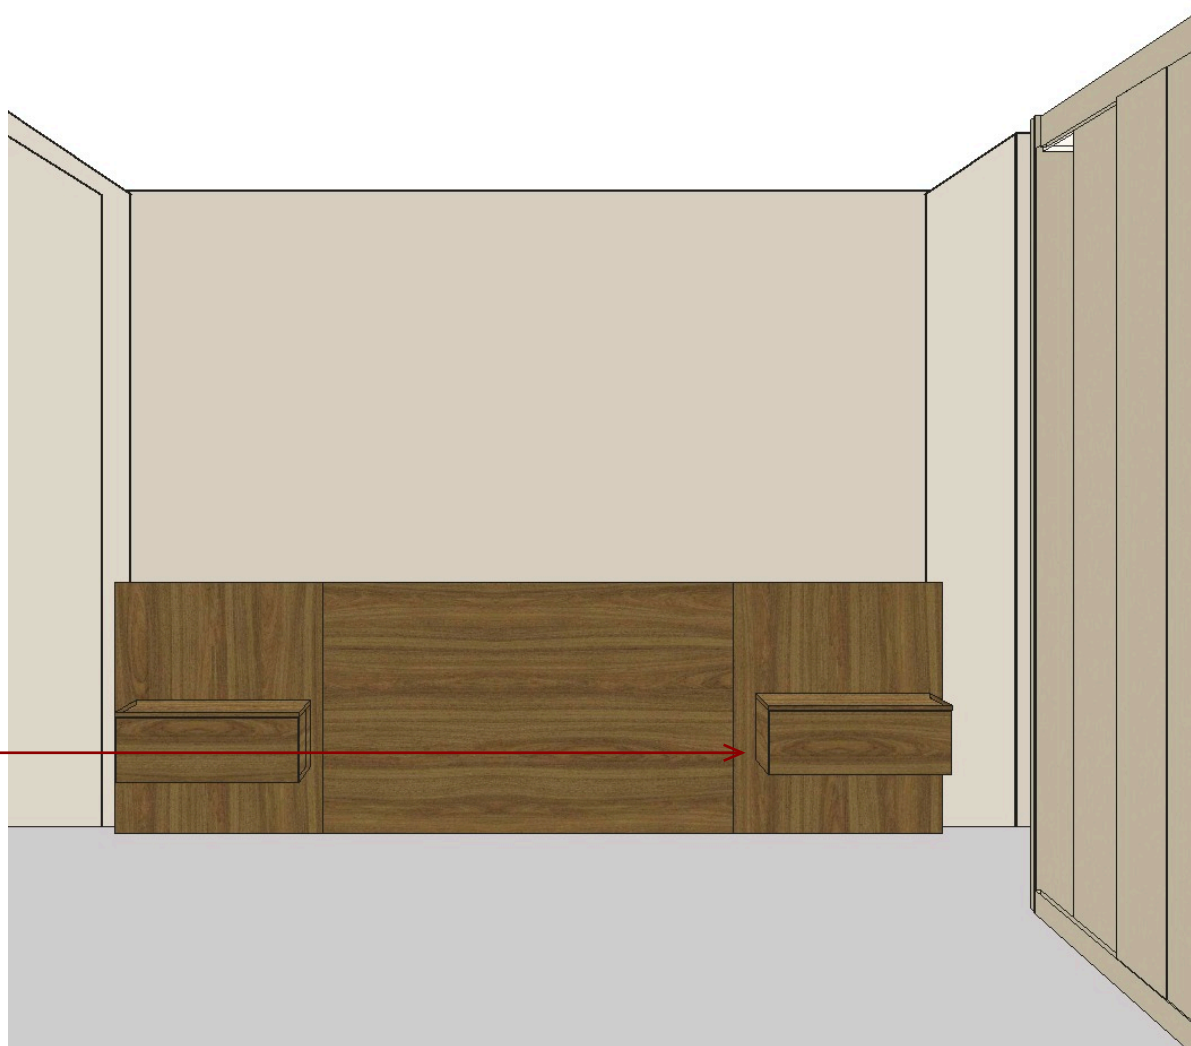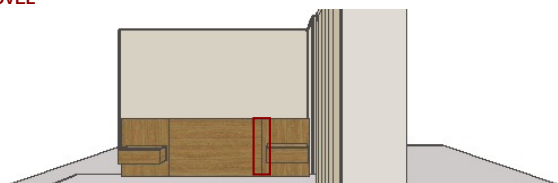



CLIENTE: **PRISCILA CLAUDINO**

AMBIENTE: **Suíte Casal**

PROJETISTA TÉCNICO: **JOÃO FELIPE SANTOS**

ARQUITETA: **FERNANDA**

**ATENÇÃO:**

DECLARO ESTAR DE ACORDO COM ESTE PROJETO E COM AS MEDIDAS NELE DESCRITAS E CIENTE DE QUE NELE CONSTAM APENAS PEÇAS E MÓDULOS DA EMPRESA, SENDO QUE OS DEMAIS ITENS SÃO MERAMENTE ILUSTRATIVOS (TAIS COMO ELETROS, COLCHÕES, GRANITOS E DECORAÇÕES NO GERAL).

ASS: \_\_\_\_\_

**PRANCHA  
12**

**PEÇA ESCONDIDA · Painel Branco MDF · VISTA C**

**PEÇA ESCONDIDA · Painel Branco MDF**



**POSIÇÃO NO MÓVEL**





CLIENTE: **PRISCILA CLAUDINO**

AMBIENTE: **Suíte Casal**

PROJETISTA TÉCNICO: **JOÃO FELIPE SANTOS**

ARQUITETA: **FERNANDA**

**ATENÇÃO:**

DECLARO ESTAR DE ACORDO COM ESTE PROJETO E COM AS MEDIDAS NELE DESCRITAS E CIENTE DE QUE NELE CONSTAM APENAS PEÇAS E MÓDULOS DA EMPRESA, SENDO QUE OS DEMAIS ITENS SÃO MERAMENTE ILUSTRATIVOS (TAIS COMO ELETROS, COLCHÕES, GRANITOS E DECORAÇÕES NO GERAL).

ASS: \_\_\_\_\_



**PRANCHA  
13**

**PEÇA ESCONDIDA · Painel Branco MDF · VISTA C**

**PEÇA ESCONDIDA · Painel Branco MDF**



**POSIÇÃO NO MÓVEL**

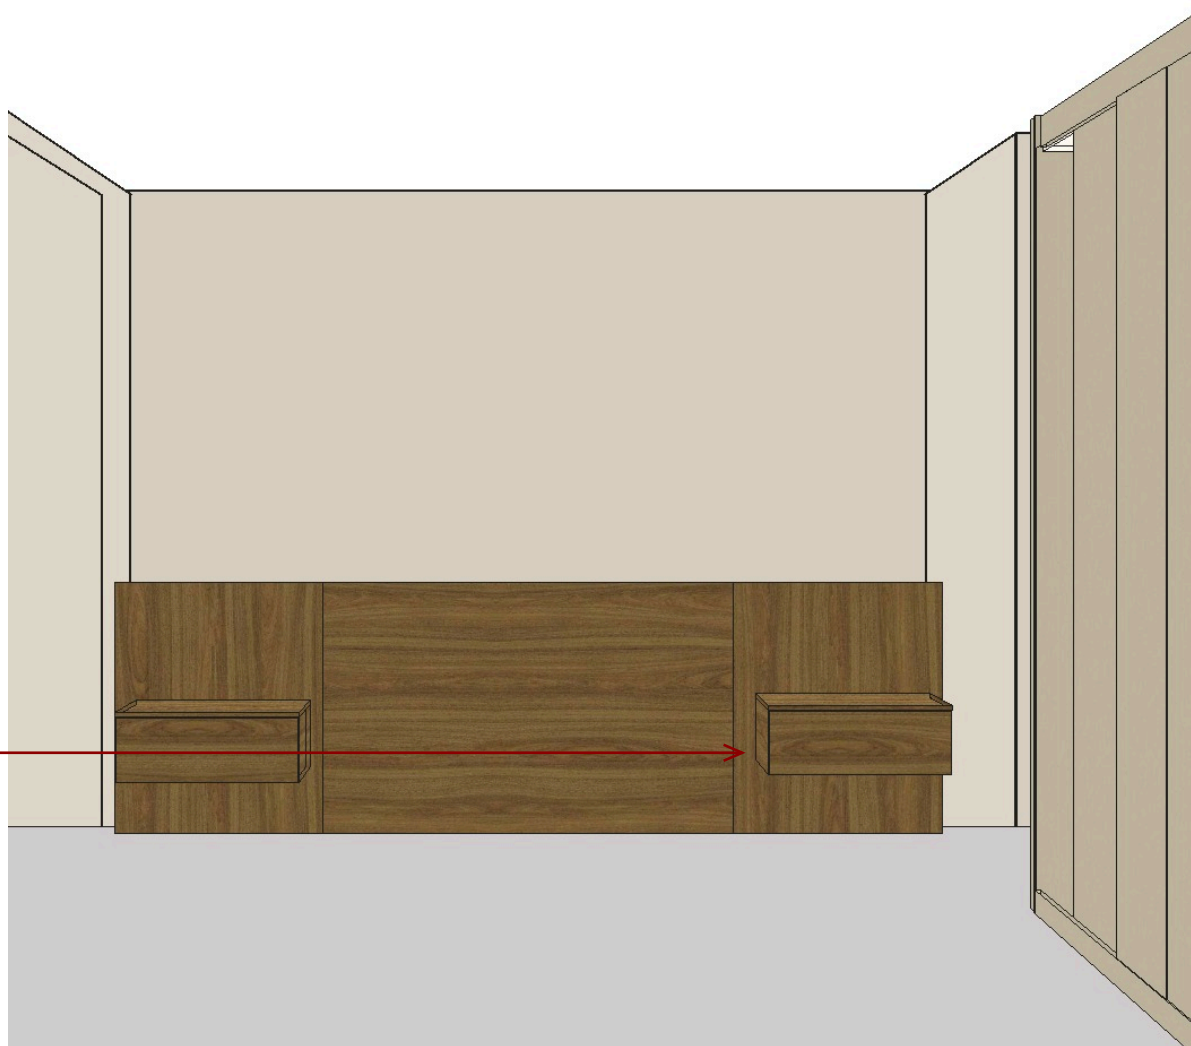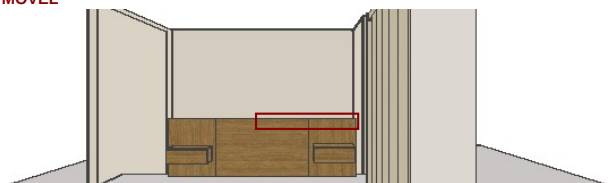



CLIENTE: **PRISCILA CLAUDINO**

AMBIENTE: **Suíte Casal**

PROJETISTA TÉCNICO: **JOÃO FELIPE SANTOS**

ARQUITETA: **FERNANDA**

**ATENÇÃO:**


DECLARO ESTAR DE ACORDO COM ESTE PROJETO E COM AS MEDIDAS NELE DESCRITAS E CIENTE DE QUE NELE CONSTAM APENAS PEÇAS E MÓDULOS DA EMPRESA, SENDO QUE OS DEMAIS ITENS SÃO MERAMENTE ILUSTRATIVOS (TAIS COMO ELETROS, COLCHÕES, GRANITOS E DECORAÇÕES NO GERAL).

ASS.: \_\_\_\_\_

# PRANCHA 14

## MÓDULOS E PAINÉIS - VISTA D

| Item | Descrição                           | Dimensão      |
|------|-------------------------------------|---------------|
| 1    | Armário c/ Portas de Giro c/ Rodapé | 2424x2540x560 |
| 2    | Tamponamento Inferior               | 2428x18x80    |
| 3    | Tamponamento Inferior               | 2645x18x70    |
| 4    | Tamponamento Inferior               | 2645x18x100   |
| 5    | Tamponamento Inferior               | 2424x18x100   |

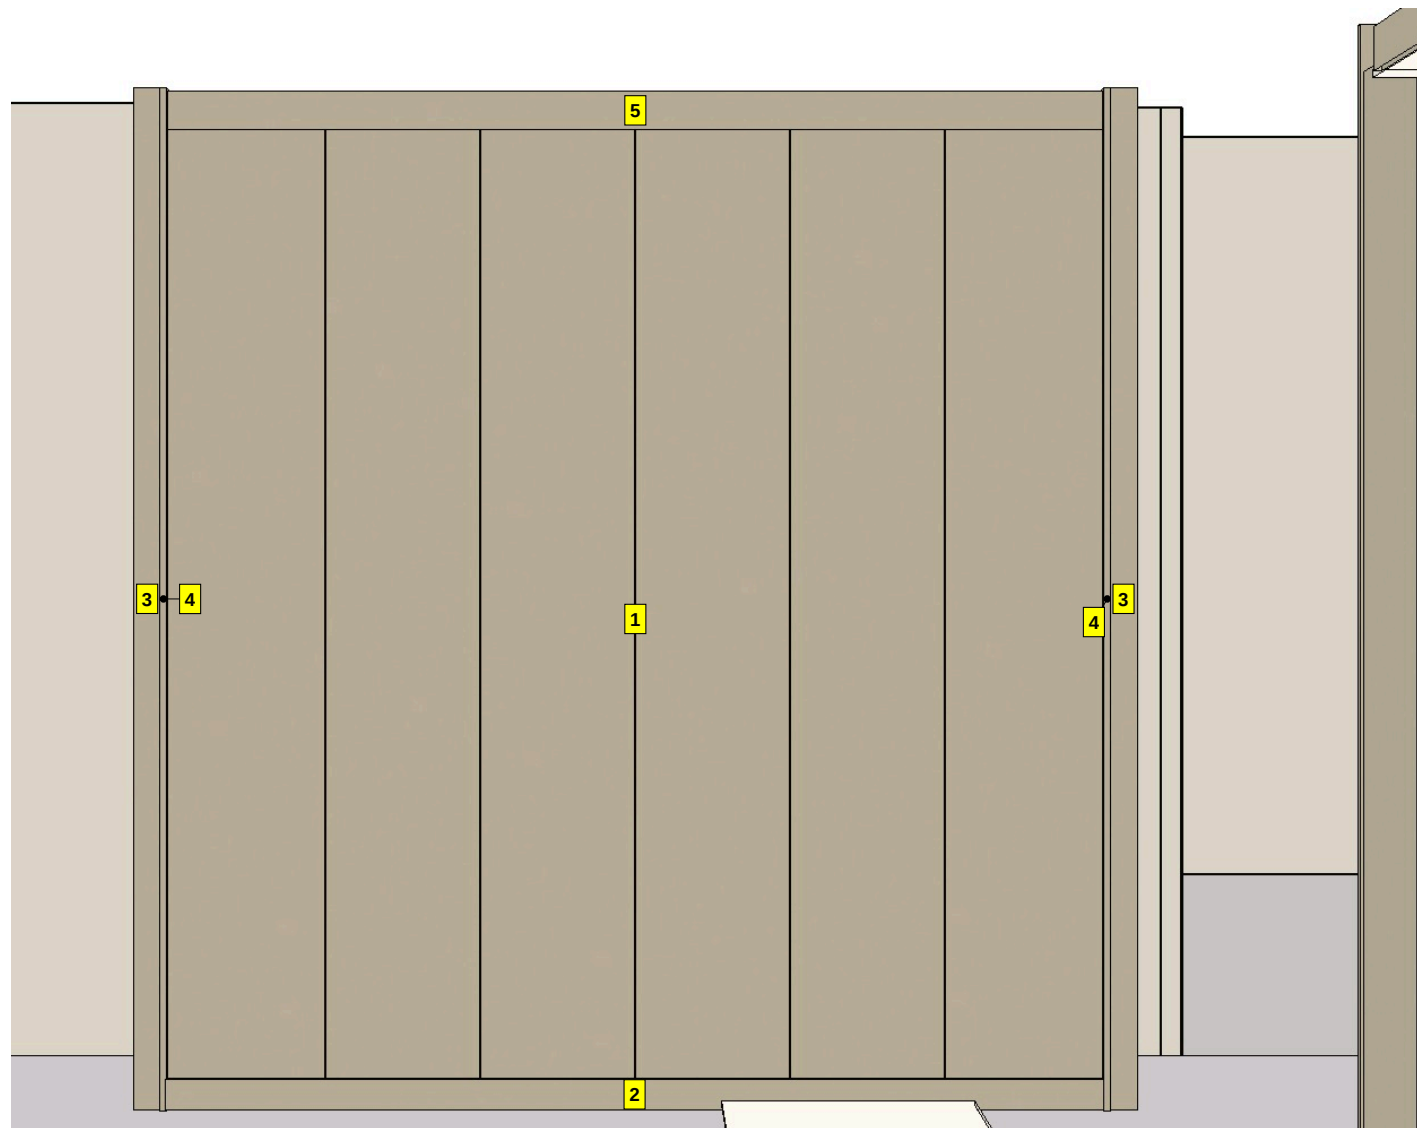



CLIENTE: **PRISCILA CLAUDINO**

AMBIENTE: **Suíte Casal**

PROJETISTA TÉCNICO: **JOÃO FELIPE SANTOS**

ARQUITETA: **FERNANDA**


**ATENÇÃO:**

DECLARO ESTAR DE ACORDO COM ESTE PROJETO E COM AS MEDIDAS NELE DESCRITAS E CIENTE DE QUE NELE CONSTAM APENAS PEÇAS E MÓDULOS DA EMPRESA, SENDO QUE OS DEMAIS ITENS SÃO MERAMENTE ILUSTRATIVOS (TAIS COMO ELETROS, COLCHÕES, GRANITOS E DECORAÇÕES NO GERAL).


ASS:.. \_\_\_\_\_

# PRANCHA 15

## MEDIDAS E ALTURAS - VISTA A / VISTA B

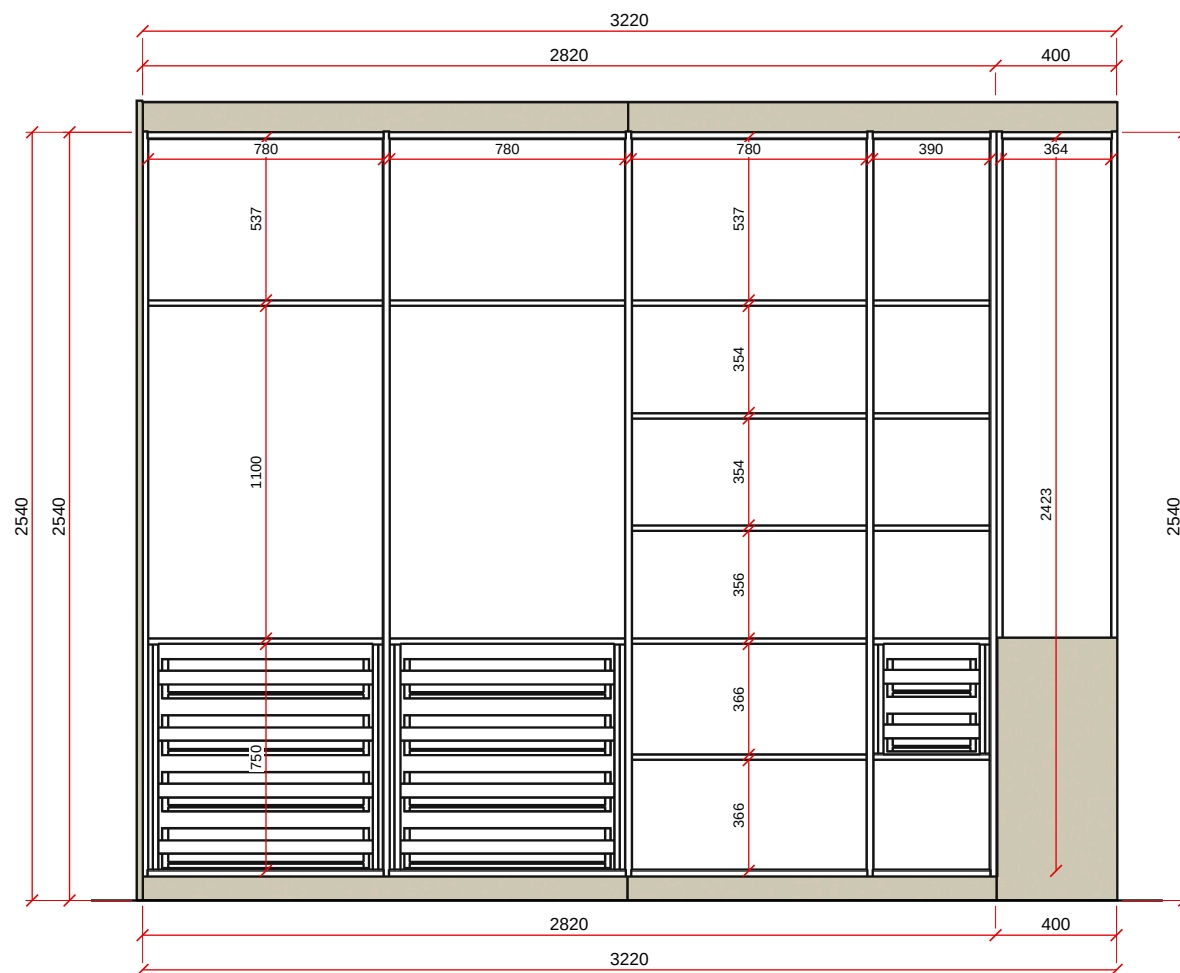

VISTA A - ESC. 1:25

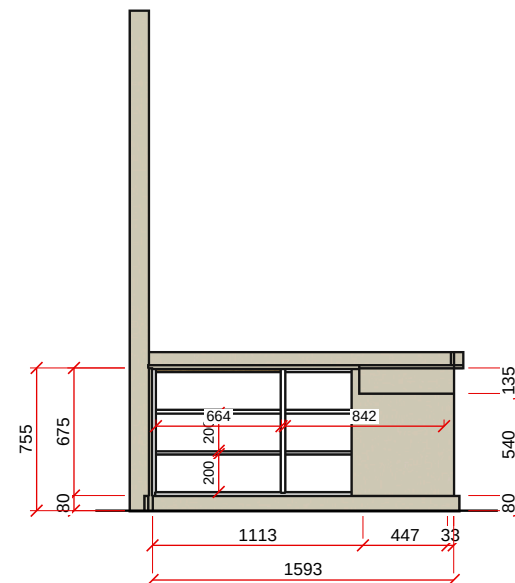

VISTA B - ESC. 1:40





CLIENTE: **PRISCILA CLAUDINO**

AMBIENTE: **Suíte Casal**

PROJETISTA TÉCNICO: **JOÃO FELIPE SANTOS**

ARQUITETA: **FERNANDA**


**ATENÇÃO:**

DECLARO ESTAR DE ACORDO COM ESTE PROJETO E COM AS MEDIDAS NELE DESCRITAS E CIENTE DE QUE NELE CONSTAM APENAS PEÇAS E MÓDULOS DA EMPRESA, SENDO QUE OS DEMAIS ITENS SÃO MERAMENTE ILUSTRATIVOS (TAIS COMO ELETROS, COLCHÕES, GRANITOS E DECORAÇÕES NO GERAL).


ASS.: \_\_\_\_\_

# PRANCHA 16

## MEDIDAS E ALTURAS - VISTA C / VISTA D

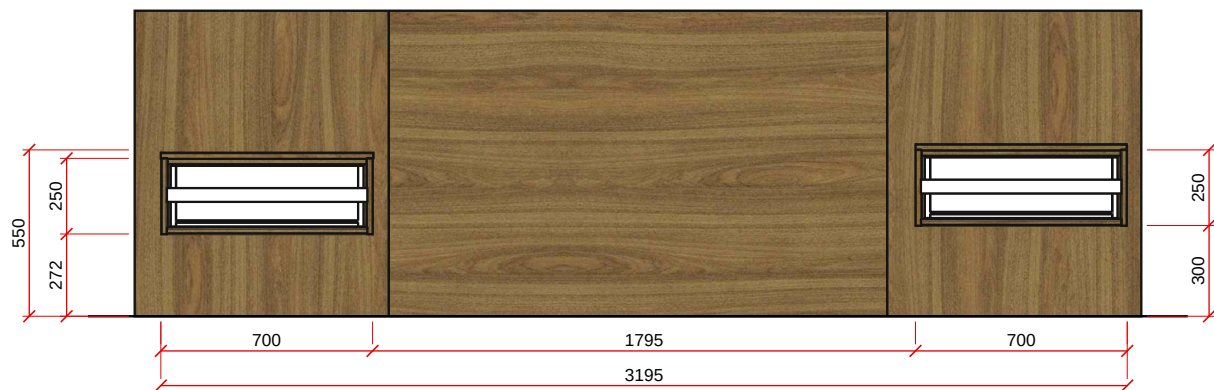

VISTA C - ESC. 1:25

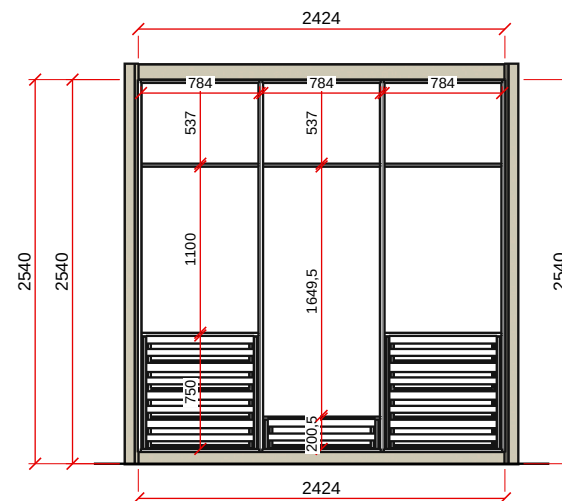

VISTA D - ESC. 1:50



CLIENTE: **PRISCILA CLAUDINO**

AMBIENTE: **Suíte Casal**

PROJETISTA TÉCNICO: **JOÃO FELIPE SANTOS**

ARQUITETA: **FERNANDA**


**ATENÇÃO:**

DECLARO ESTAR DE ACORDO COM ESTE PROJETO E COM AS MEDIDAS NELE DESCRITAS E CIENTE DE QUE NELE CONSTAM APENAS PEÇAS E MÓDULOS DA EMPRESA, SENDO QUE OS DEMAIS ITENS SÃO MERAMENTE ILUSTRATIVOS (TAIS COMO ELETROS, COLCHÕES, GRANITOS E DECORAÇÕES NO GERAL).

ASS.: \_\_\_\_\_

# PRANCHA 17

## MEDIDAS - ITEM ESPECIAL: DIVISORIA

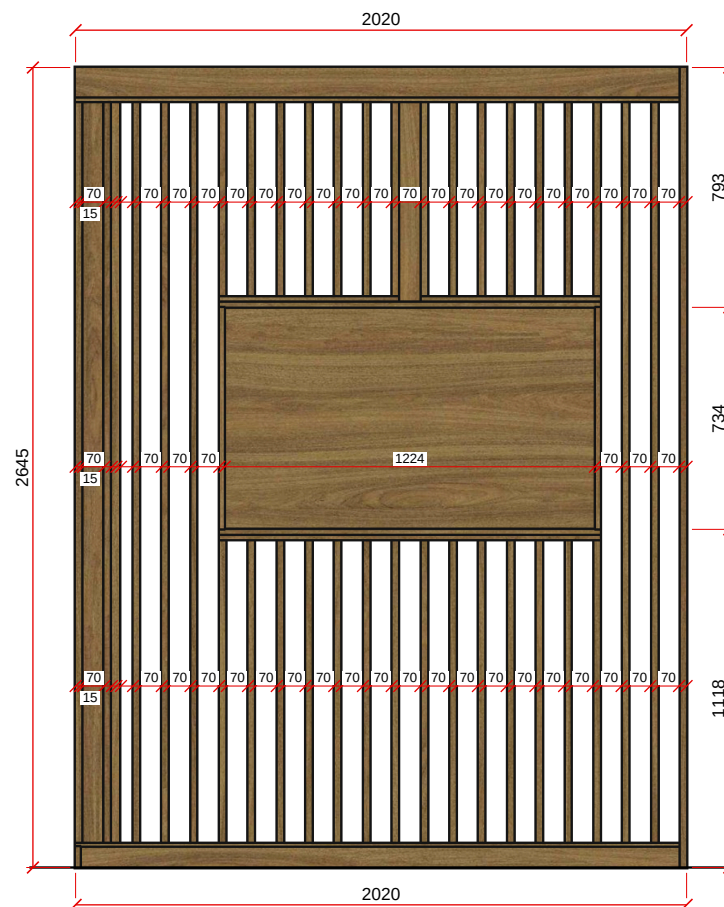

**DIVISORIA - ESC. 1:25**



CLIENTE: **PRISCILA CLAUDINO**

AMBIENTE: **Suíte Casal**

PROJETISTA TÉCNICO: **JOÃO FELIPE SANTOS**

ARQUITETA: **FERNANDA**


**ATENÇÃO:**

DECLARO ESTAR DE ACORDO COM ESTE PROJETO E COM AS MEDIDAS NELE DESCRITAS E CIENTE DE QUE NELE CONSTAM APENAS PEÇAS E MÓDULOS DA EMPRESA, SENDO QUE OS DEMAIS ITENS SÃO MERAMENTE ILUSTRATIVOS (TAIS COMO ELETROS, COLCHÕES, GRANITOS E DECORAÇÕES NO GERAL).

ASS.: \_\_\_\_\_

**PRANCHA  
18**

**MEDIDAS - ITEM ESPECIAL: DIVISOR TALHER**

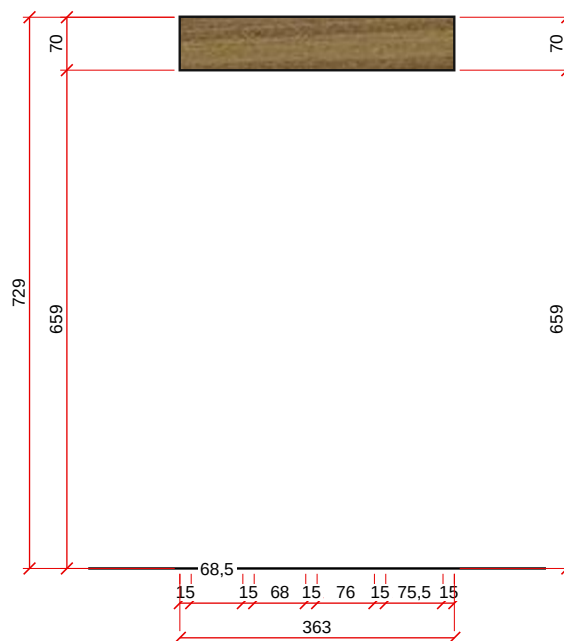

**DIVISOR TALHER - ESC. 1:10**