



RAFAEL CLARET

EXECUTIVO - SUITE_CASAL



CLIENTE: **RAFAEL CLARET**

AMBIENTE: **Suite_Casal**

PROJETISTA TÉCNICO: **JOÃO FELIPE SANTOS**

ARQUITETA: **FERNANDA**

ATENÇÃO:

DECLARO ESTAR DE ACORDO COM ESTE PROJETO E COM AS MEDIDAS NELE DESCRITAS E CIENTE DE QUE NELE CONSTAM APENAS PEÇAS E MÓDULOS DA EMPRESA, SENDO QUE OS DEMAIS ITENS SÃO MERAMENTE ILUSTRATIVOS (TAIS COMO ELETROS, COLCHÕES, GRANITOS E DECORAÇÕES NO GERAL).

ASS: _____

**PRANCHA
02**

CONTRATO

LEIA COM ATENÇÃO

1- CLIENTE ESTÁ RECEBENDO UMA CÓPIA DOS PROJETOS ADQUIRIDOS E ESTÁ DE ACORDO COM AS INFORMAÇÕES APONTADAS SOBRE MODELO, COR, ACABAMENTO, ESTRUTURAS, ACESSÓRIOS E CONDIÇÕES QUE FAZEM PARTE DESTES PROJETOS EXECUTIVOS.

2- O MESMO FOI ELABORADO CONSIDERANDO AS MEDIDAS REAIS DESTES AMBIENTES, SE HOUVER ALGUMA ALTERAÇÃO NO PÉ DIREITO OU NAS PAREDES, REFERENTE À INSTALAÇÃO DE MOLDURAS DE GESSO, RODAPÉS, MODIFICAÇÃO EM INSTALAÇÃO DA MODULAÇÃO NO DIA DA MONTAGEM, A EMPRESA NÃO SE RESPONSABILIZA QUANTO A FUTUROS CONTRATEMPOS DEVIDOS ÀS ALTERAÇÕES. CABE AO CLIENTE AVISAR O PROJETISTA ANTES DA MEDIÇÃO FINAL PARA ADEQUAÇÃO DA MODULAÇÃO.

3- SE HOUVER GRANITO NOS AMBIENTES, A MEDIÇÃO FINAL SE DARÁ APÓS A CONCLUSÃO DA INSTALAÇÃO DOS MESMOS, OU INSTALAR APÓS A MONTAGEM DOS MÓVEIS.

4- SE HOUVER REDUÇÃO OU RECORTES NOS MÓDULOS, O CLIENTE TOMA CIÊNCIA QUE OS AJUSTES SERÃO EXECUTADOS NO LOCAL, QUE DEVE ESTAR LIVRE DE OBJETOS E PESSOAS QUE POSSAM SOFRER DE ALGUMA MANEIRA COM O PÓ DECORRENTE DESSES AJUSTES E QUALQUER OBJETO QUE NÃO POSSA SER RETIRADO DEVE ESTAR DEVIDAMENTE COBERTO. POR NÃO POSSUIR PROFISSIONAIS ESPECIALIZADOS EM INSTALAÇÕES DE ELETROS, INSTALAÇÕES HIDRÁULICAS, A EMPRESA NÃO EFETUARÁ ESSE TIPO DE SERVIÇO. É NECESSÁRIO FORNECER AS PLANTAS DE INSTALAÇÃO ELÉTRICA E HIDRÁULICA DOS AMBIENTES NO DIA DA MONTAGEM, É NECESSÁRIO O ACOMPANHAMENTO DO CLIENTE OU UM RESPONSÁVEL PELA OBRA, MAIOR QUE 18 ANOS PARA TIRAR EVENTUAIS DÚVIDAS DOS MONTADORES REFERENTE AOS LOCAIS ONDE É POSSÍVEL FAZER FURAÇÕES. A ASSINATURA DESSE PROJETO SUBSTITUI QUALQUER PROJETO ANTERIOR.

5- O CLIENTE DECLARA ESTAR CIENTE QUE CASO O PROJETO ENVOLVA ELETROS, OS MESMOS DEVERÃO ESTAR NO LOCAL NO DIA DA MONTAGEM PARA ADEQUAÇÃO DOS NICHOS NECESSÁRIOS, E SE NÃO COMPROU OS ELETROS, SE RESPONSABILIZA EM ADQUIRIR OS MESMOS DENTRO DAS MEDIDAS ESPECIFICADAS NESTE PROJETO.

6- DECLARO ESTAR DE ACORDO COM ESTE PROJETO E COM AS MEDIDAS NELE DESCRITAS E CIENTE DE QUE NELE CONSTAM APENAS PEÇAS E MÓDULOS DA EMPRESA DUO PLANEJADOS, SENDO QUE OS DEMAIS ITENS SÃO MERAMENTE ILUSTRATIVOS (TAIS COMO ELETROS, COLCHÕES, GRANITOS E DECORAÇÕES EM GERAL).



CLIENTE: **RAFAEL CLARET**

AMBIENTE: **Suite_Casal**

PROJETISTA TÉCNICO: **JOÃO FELIPE SANTOS**

ARQUITETA: **FERNANDA**

ATENÇÃO:

DECLARO ESTAR DE ACORDO COM ESTE PROJETO E COM AS MEDIDAS NELE DESCRITAS E CIENTE DE QUE NELE CONSTAM APENAS PEÇAS E MÓDULOS DA EMPRESA, SENDO QUE OS DEMAIS ITENS SÃO MERAMENTE ILUSTRATIVOS (TAIS COMO ELETROS, COLCHÕES, GRANITOS E DECORAÇÕES NO GERAL).

ASS.: _____

**PRANCHA
03**

PLANTA - ESPECIFICAÇÕES DO PROJETO

ESPECIFICAÇÕES DO PROJETO

CORES E ACABAMENTOS:

Caixa Módulos (Interno): **Branco, Metallic Sued**

Portas e Frentes: **Metallic Sued, Branco**

Tamponamentos: **Metallic Sued**

Painéis e Tampas: **Metallic Sued**

Puxadores: **Fosco**

Portas de Vidro:

FERRAGENS E ACESSÓRIOS:

Dobradiças:

Dobradiça Reta c/ Amortecedor, Dobradiça Curva c/ Amortecedor

Corrediças:

Kit Corrediça Telescópica Total 450mm, Kit Corrediça Telescópica Total 250mm, Kit Corrediça Telescópica Total 300mm

Puxadores:

Puxador Linear (15, 18 e 20mm) Pino Fosco - 150mm

Ferragens especiais: **Cabideiro Tubo s/ Reforço**

ESPESSURAS:


Caixa Módulos (Interno): **18mm (fundo 6mm e 18mm)**

Prateleiras internas: **18mm**

Portas e Frentes: **18mm**

Tamponamentos: **18mm**

Painéis e Tampas e perfil: **18mm**

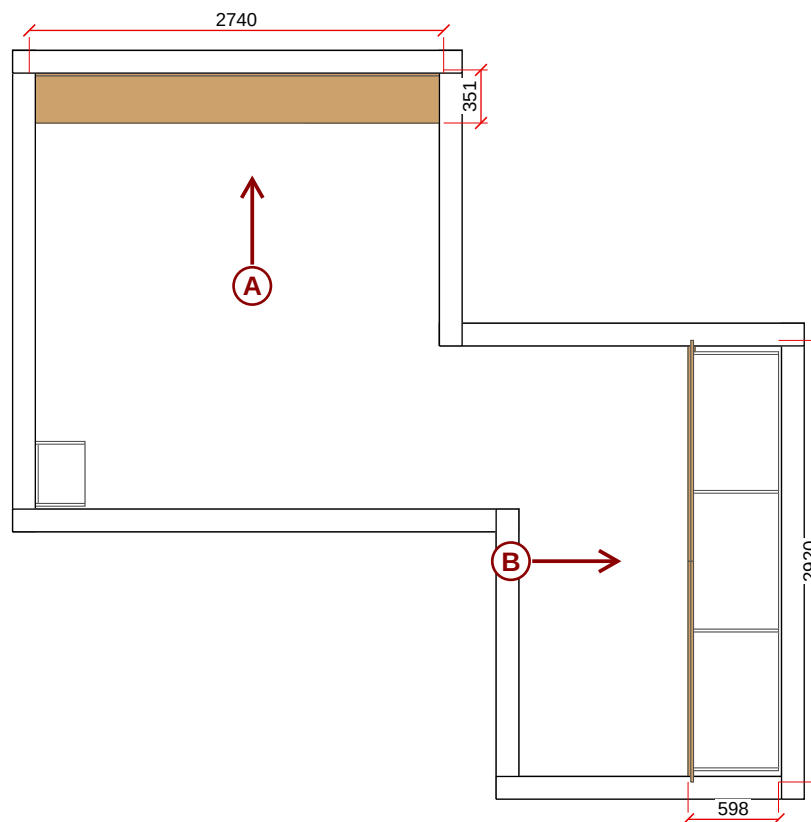

PLANTA BAIXA - ESC. 1:50



CLIENTE: **RAFAEL CLARET**

AMBIENTE: **Suite_Casal**

PROJETISTA TÉCNICO: **JOÃO FELIPE SANTOS**

ARQUITETA: **FERNANDA**

ATENÇÃO:


DECLARO ESTAR DE ACORDO COM ESTE PROJETO E COM AS MEDIDAS NELE DESCRITAS E CIENTE DE QUE NELE CONSTAM APENAS PEÇAS E MÓDULOS DA EMPRESA, SENDO QUE OS DEMAIS ITENS SÃO MERAMENTE ILUSTRATIVOS (TAIS COMO ELETROS, COLCHÕES, GRANITOS E DECORAÇÕES NO GERAL).

ASS: _____


**PRANCHA
04**

VISÃO GERAL DOS MÓVEIS

VISTA A

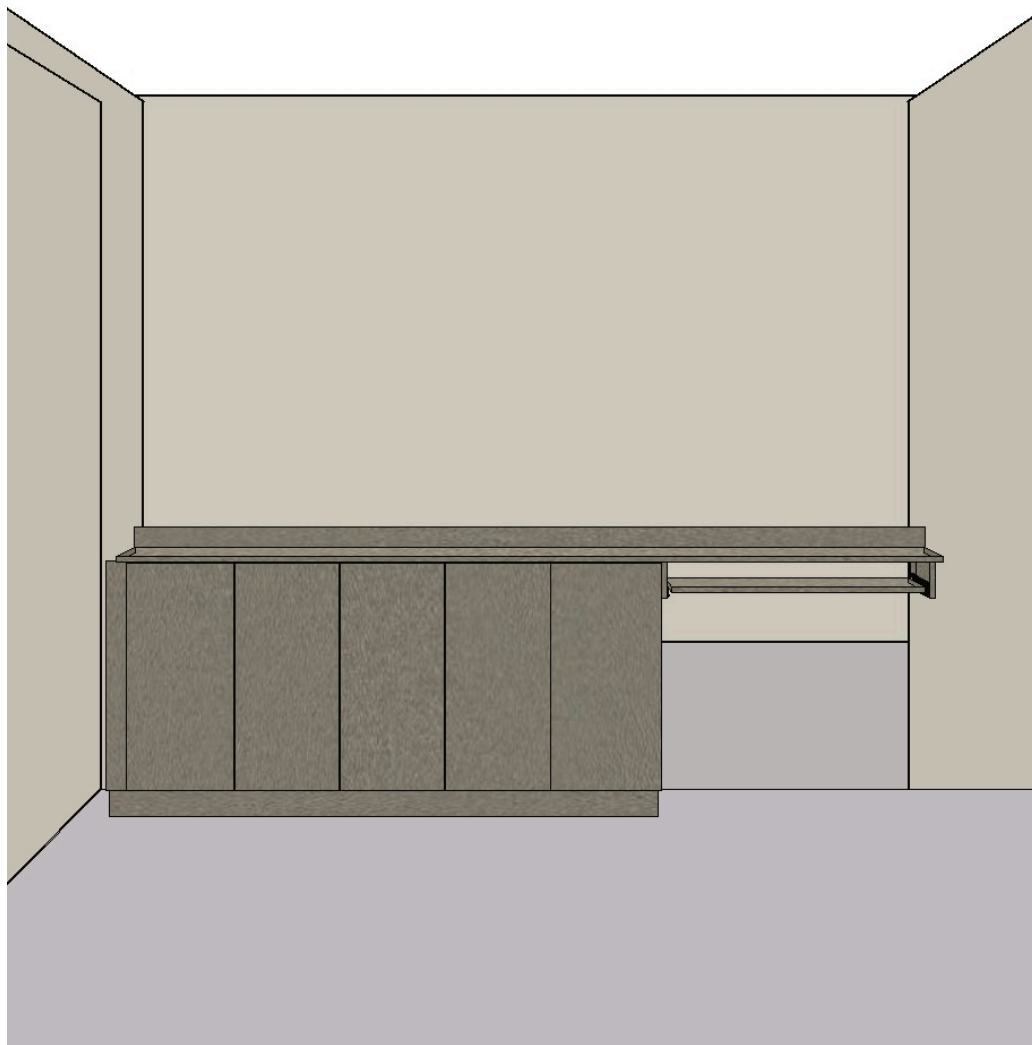

VISTA B

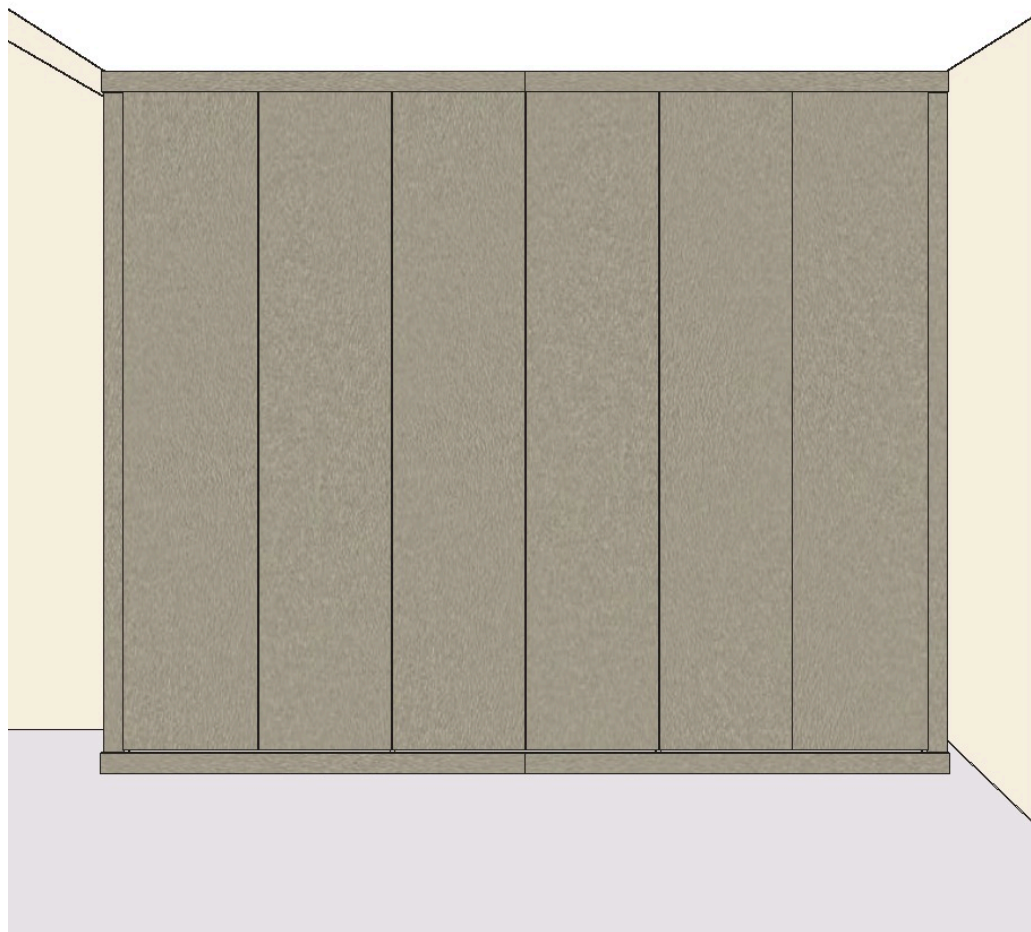



CLIENTE: **RAFAEL CLARET**

AMBIENTE: **Suite_Casal**

PROJETISTA TÉCNICO: **JOÃO FELIPE SANTOS**

ARQUITETA: **FERNANDA**

ATENÇÃO:

DECLARO ESTAR DE ACORDO COM ESTE PROJETO E COM AS MEDIDAS NELE DESCRITAS E CIENTE DE QUE NELE CONSTAM APENAS PEÇAS E MÓDULOS DA EMPRESA, SENDO QUE OS DEMAIS ITENS SÃO MERAMENTE ILUSTRATIVOS (TAIS COMO ELETROS, COLCHÕES, GRANITOS E DECORAÇÕES NO GERAL).

ASS.: _____

**PRANCHA
05**



MÓDULOS E PAINÉIS - VISTA A

Item	Descrição	Dimensão
1	Balcão Inferior	1750x750x307
2	Painel Metallic Sued MDF	829x18x300
3	Tamponamento	330x18x120
4	Tamponamento	300x18x90
5	Tamponamento	1800x18x90
6	Tamponamento	2700x18x70
7	Tamponamento	2700x18x330
8	Tamponamento	750x18x70

PEÇA ESCONDIDA - Tamponamento



POSIÇÃO NO MÓVEL

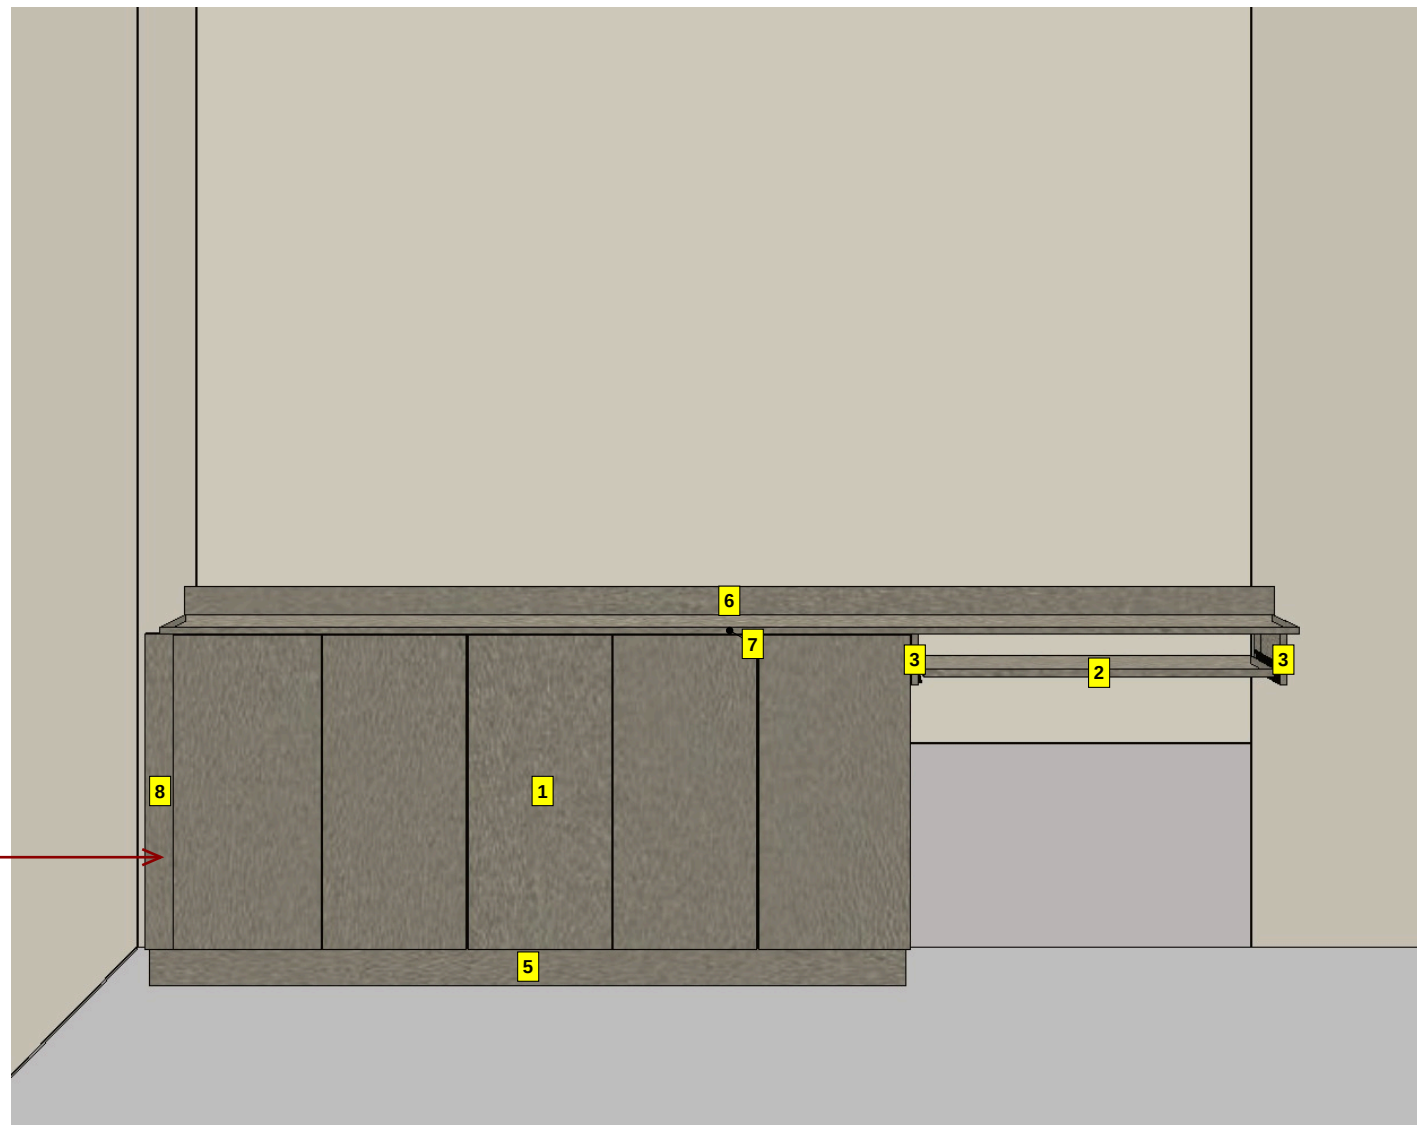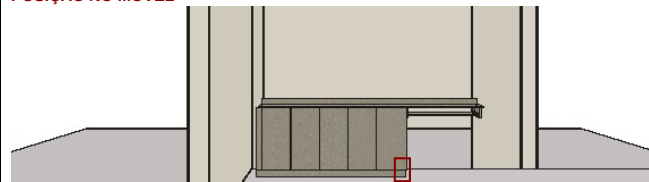



CLIENTE: **RAFAEL CLARET**

AMBIENTE: **Suite_Casal**

PROJETISTA TÉCNICO: **JOÃO FELIPE SANTOS**

ARQUITETA: **FERNANDA**

ATENÇÃO:


DECLARO ESTAR DE ACORDO COM ESTE PROJETO E COM AS MEDIDAS NELE DESCRITAS E CIENTE DE QUE NELE CONSTAM APENAS PEÇAS E MÓDULOS DA EMPRESA, SENDO QUE OS DEMAIS ITENS SÃO MERAMENTE ILUSTRATIVOS (TAIS COMO ELETROS, COLCHÕES, GRANITOS E DECORAÇÕES NO GERAL).

ASS.: _____

**PRANCHA
06**

MÓDULOS E PAINÉIS - VISTA B

Item	Descrição	Dimensão
1	Armário c/ Portas de Giro c/ Rodapé	2770x2350x580
2	Tamponamento	1460x18x70
3	Tamponamento	2350x18x70

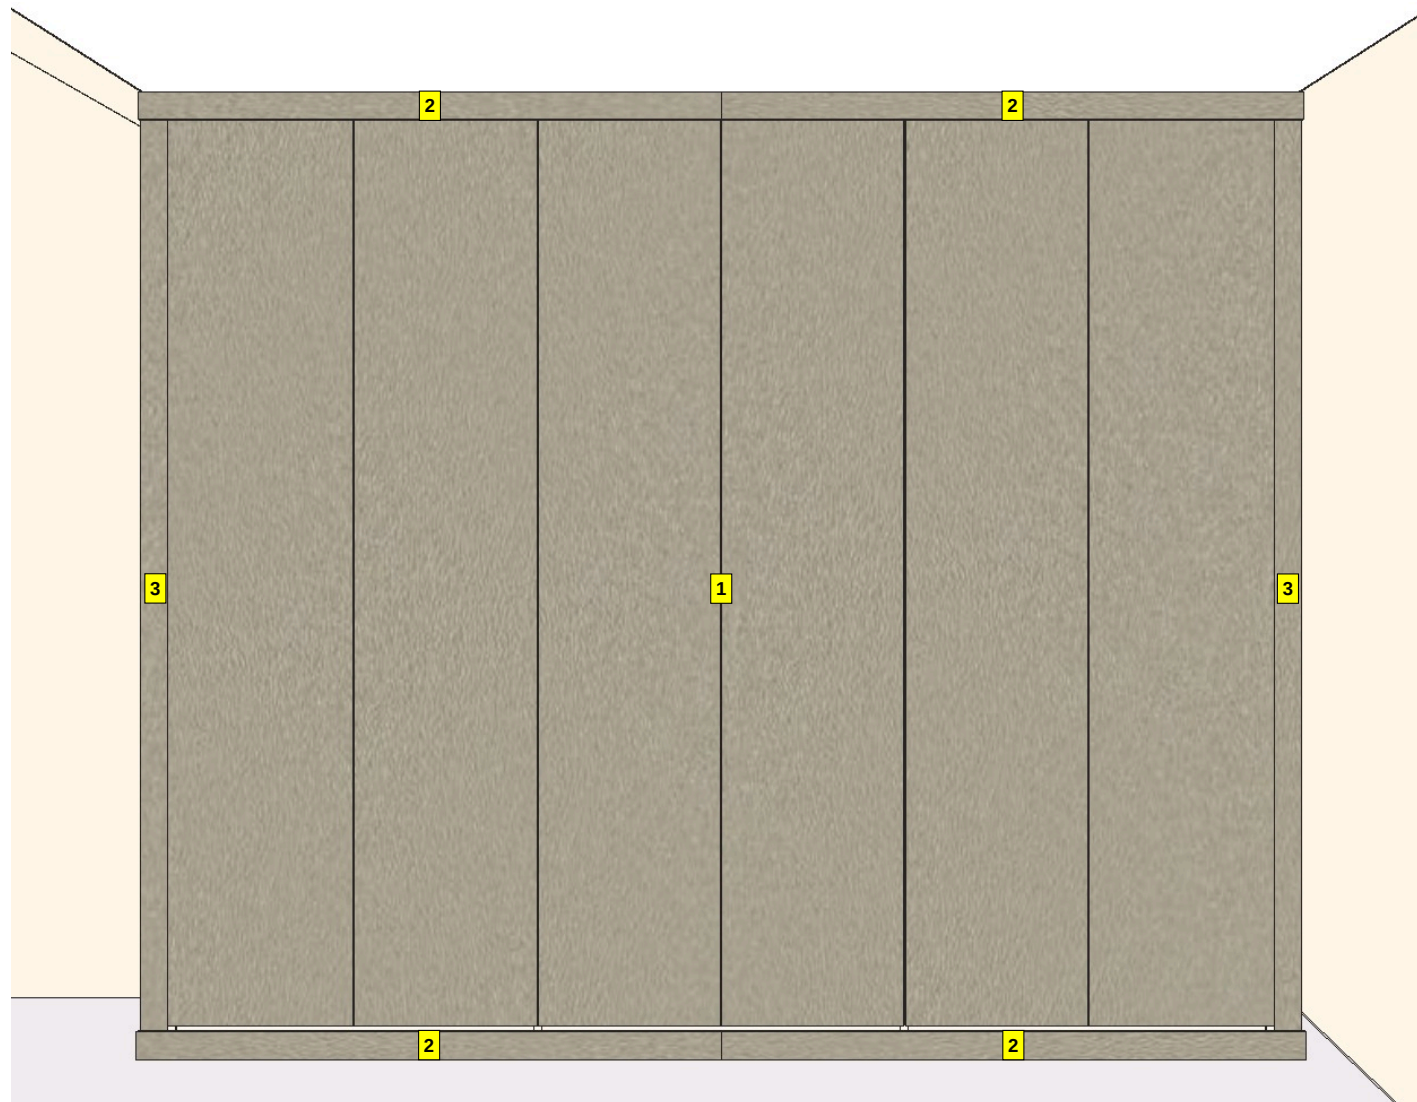



CLIENTE: **RAFAEL CLARET**

AMBIENTE: **Suite_Casal**

PROJETISTA TÉCNICO: **JOÃO FELIPE SANTOS**

ARQUITETA: **FERNANDA**


ATENÇÃO:

DECLARO ESTAR DE ACORDO COM ESTE PROJETO E COM AS MEDIDAS NELE DESCRITAS E CIENTE DE QUE NELE CONSTAM APENAS PEÇAS E MÓDULOS DA EMPRESA, SENDO QUE OS DEMAIS ITENS SÃO MERAMENTE ILUSTRATIVOS (TAIS COMO ELETROS, COLCHÕES, GRANITOS E DECORAÇÕES NO GERAL).


ASS.: _____

**PRANCHA
07**

MEDIDAS E ALTURAS - VISTA A / VISTA B

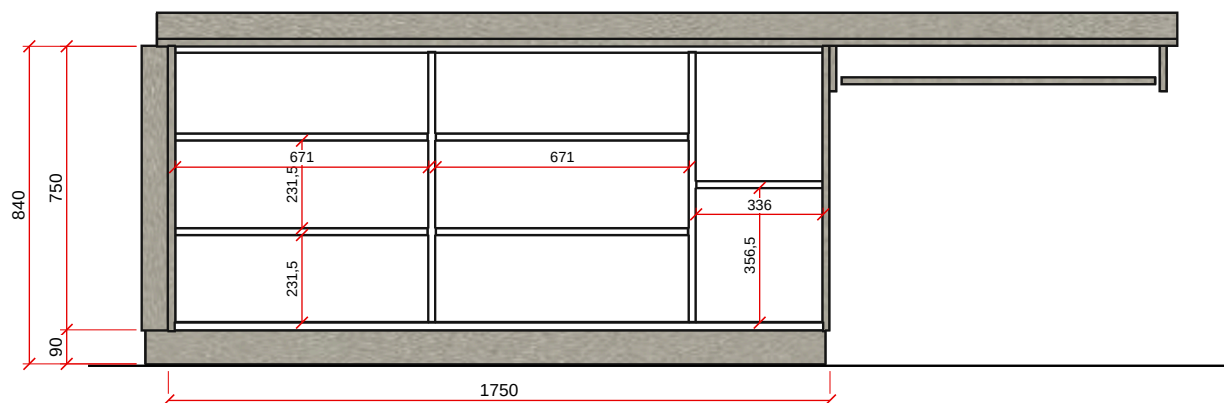

VISTA A - ESC. 1:20

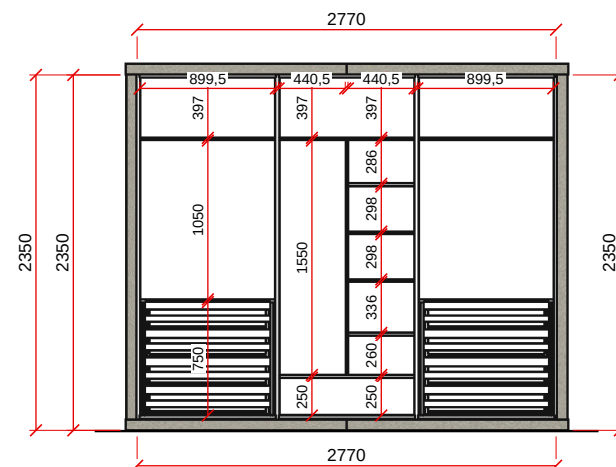

VISTA B - ESC. 1:50



CLIENTE: **RAFAEL CLARET**

AMBIENTE: **Suite_Casal**

PROJETISTA TÉCNICO: **JOÃO FELIPE SANTOS**

ARQUITETA: **FERNANDA**


ATENÇÃO:

DECLARO ESTAR DE ACORDO COM ESTE PROJETO E COM AS MEDIDAS NELE DESCRITAS E CIENTE DE QUE NELE CONSTAM APENAS PEÇAS E MÓDULOS DA EMPRESA, SENDO QUE OS DEMAIS ITENS SÃO MERAMENTE ILUSTRATIVOS (TAIS COMO ELETROS, COLCHÕES, GRANITOS E DECORAÇÕES NO GERAL).

ASS: _____

**PRANCHA
08**

MEDIDAS - ITEM ESPECIAL: PAINEL

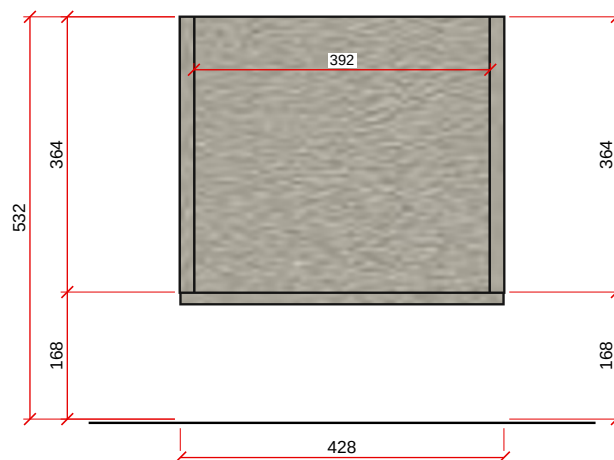

PAINEL - ESC. 1:10