



---

**JAQUELINE DA SILVA**

EXECUTIVO - CLOSET



CLIENTE: **JAQUELINE DA SILVA**

AMBIENTE: **Closet**

PROJETISTA TÉCNICO: **JOÃO FELIPE SANTOS**

ARQUITETA: **FERNANDA**

**ATENÇÃO:**

DECLARO ESTAR DE ACORDO COM ESTE PROJETO E COM AS MEDIDAS NELE DESCRITAS E CIENTE DE QUE NELE CONSTAM APENAS PEÇAS E MÓDULOS DA EMPRESA, SENDO QUE OS DEMAIS ITENS SÃO MERAMENTE ILUSTRATIVOS (TAIS COMO ELETROS, COLCHÕES, GRANITOS E DECORAÇÕES NO GERAL).

ASS: \_\_\_\_\_

**PRANCHA  
02**

## **CONTRATO**

### **LEIA COM ATENÇÃO**

**1-** CLIENTE ESTÁ RECEBENDO UMA CÓPIA DOS PROJETOS ADQUIRIDOS E ESTÁ DE ACORDO COM AS INFORMAÇÕES APONTADAS SOBRE MODELO, COR, ACABAMENTO, ESTRUTURAS, ACESSÓRIOS E CONDIÇÕES QUE FAZEM PARTE DESTES PROJETOS EXECUTIVOS.

**2-** O MESMO FOI ELABORADO CONSIDERANDO AS MEDIDAS REAIS DESTE AMBIENTE, SE HOUVER ALGUMA ALTERAÇÃO NO PÉ DIREITO OU NAS PAREDES, REFERENTE A INSTALAÇÃO DE MOLDURAS DE GESSO, RODAPÉS, MODIFICAÇÃO EM INSTALAÇÃO DA MODULAÇÃO NO DIA DA MONTAGEM, A EMPRESA NÃO SE RESPONSABILIZA QUANTO A FUTUROS CONTRATEMPOS DEVIDOS A TAIS ALTERAÇÕES. CABE AO CLIENTE AVISAR O PROJETISTA ANTES DA MEDIÇÃO FINAL PARA ADEQUAÇÃO DA MODULAÇÃO.

**3-** SE HOUVER GRANITO NOS AMBIENTES, A MEDIÇÃO FINAL SE DARÁ APÓS A CONCLUSÃO DA INSTALAÇÃO DOS MESMOS, OU INSTALAR APÓS A MONTAGEM DOS MÓVEIS.

**4-** SE HOUVER REDUÇÃO OU RECORTES NOS MÓDULOS, O CLIENTE TOMA CIÊNCIA QUE OS AJUSTES SERÃO EXECUTADOS NO LOCAL, QUE DEVE ESTAR LIVRE DE OBJETOS E PESSOAS QUE POSSAM SOFRER DE ALGUMA MANEIRA COM O PÓ DECORRENTE DESSES AJUSTES E QUALQUER OBJETO QUE NÃO POSSA SER RETIRADO DEVE ESTAR DEVIDAMENTE COBERTO. POR NÃO POSSUIR PROFISSIONÁIS ESPECIALIZADOS EM INSTALAÇÕES DE ELETROS, INSTALAÇÕES HIDRÁULICAS, A EMPRESA NÃO EFETUARÁ ESSE TIPO DE SERVIÇO. É NECESSÁRIO FORNECER AS PLANTAS DE INSTALAÇÃO ELÉTRICA E HIDRÁULICA DOS AMBIENTES NO DIA DA MONTAGEM, É NECESSÁRIO O ACOMPANHAMENTO DO CLIENTE OU UM RESPONSÁVEL PELA OBRA, MAIOR QUE 18 ANOS PARA TIRAR EVENTUAIS DÚVIDAS DOS MONTADORES REFERENTE AOS LOCAIS ONDE É POSSÍVEL FAZER FURAÇÕES. A ASSINATURA DESSE PROJETO SUBSTITUI QUALQUER PROJETO ANTERIOR.

**5-** O CLIENTE DECLARA ESTAR CIENTE QUE CASO O PROJETO ENVOLVA ELETROS, OS MESMOS DEVERÃO ESTAR NO LOCAL NO DIA DA MONTAGEM PARA ADEQUAÇÃO DOS NICHOS NECESSÁRIOS, E SE NÃO COMPROU OS ELETROS, SE RESPONSABILIZA EM ADQUIRIR OS MESMOS DENTRO DAS MEDIDAS ESPECIFICADAS NESTE PROJETO.

**6-** DECLARO ESTAR DE ACORDO COM ESTE PROJETO E COM AS MEDIDAS NELE DESCRITAS E CIENTE DE QUE NELE CONSTAM APENAS PEÇAS E MÓDULOS DA EMPRESA DUO PLANEJADOS, SENDO QUE OS DEMAIS ITENS SÃO MERAMENTE ILUSTRATIVOS (TAIS COMO ELETROS, COLCHÕES, GRANITOS E DECORAÇÕES EM GERAL).



CLIENTE: **JAQUELINE DA SILVA**

AMBIENTE: **Closet**

PROJETISTA TÉCNICO: **JOÃO FELIPE SANTOS**

ARQUITETA: **FERNANDA**

**ATENÇÃO:**

DECLARO ESTAR DE ACORDO COM ESTE PROJETO E COM AS MEDIDAS NELE DESCRITAS E CIENTE DE QUE NELE CONSTAM APENAS PEÇAS E MÓDULOS DA EMPRESA, SENDO QUE OS DEMAIS ITENS SÃO MERAMENTE ILUSTRATIVOS (TAIS COMO ELETROS, COLCHÕES, GRANITOS E DECORAÇÕES NO GERAL).

ASS.: \_\_\_\_\_

**PRANCHA  
03**

## PLANTA - ESPECIFICAÇÕES DO PROJETO

### ESPECIFICAÇÕES DO PROJETO

#### CORES E ACABAMENTOS:

Caixa Módulos (Interno): **Branco**

Portas e Frentes: **Branco**

Tamponamentos:

Painéis e Tampos: **Branco**

Puxadores: **Fosco**

Portas de Vidro: **Vidro Espelho Prata · (Posição 1)**

#### FERRAGENS E ACESSÓRIOS:

Dobradiças: **Dobradiça Reta c/ Amortecedor**

Corrediças:

Puxadores: **Puxador Lee Fosco · (Posição 4)**

Ferragens especiais:

**Cabideiro Tubo s/ Reforço, Prat Sapateira, Frente Sapateira**

#### ESPESSURAS:


Caixa Módulos (Interno): **18mm (fundo 6mm)**

Prateleiras internas: **18mm**

Portas e Frentes: **18mm**

Tamponamentos:

Painéis e Tampos e perfil: **18mm**

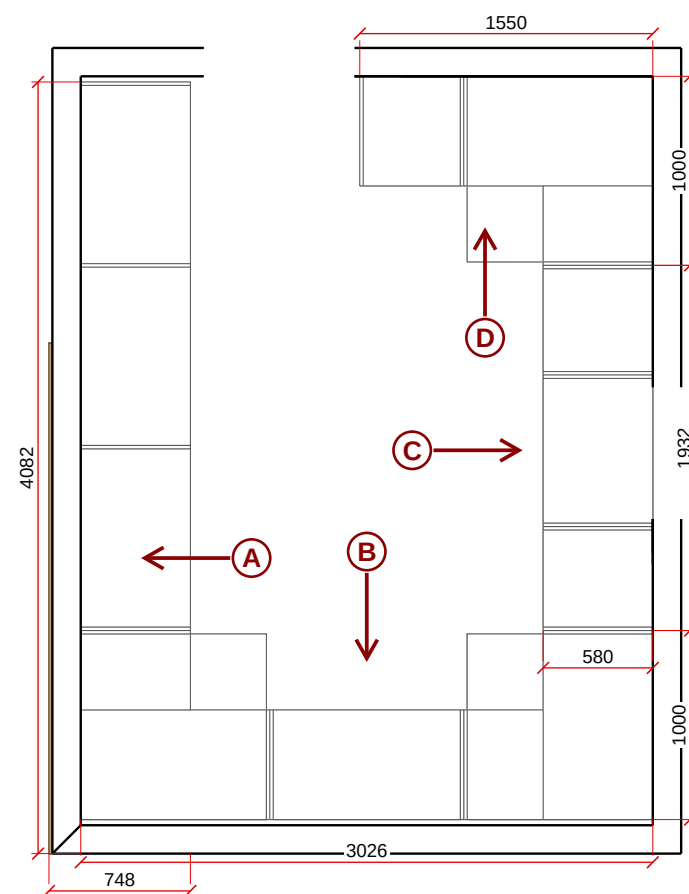

PLANTA BAIXA - ESC. 1:40



CLIENTE: **JAQUELINE DA SILVA**

AMBIENTE: **Closet**

PROJETISTA TÉCNICO: **JOÃO FELIPE SANTOS**

ARQUITETA: **FERNANDA**

**ATENÇÃO:**


DECLARO ESTAR DE ACORDO COM ESTE PROJETO E COM AS MEDIDAS NELE DESCRITAS E CIENTE DE QUE NELE CONSTAM APENAS PEÇAS E MÓDULOS DA EMPRESA, SENDO QUE OS DEMAIS ITENS SÃO MERAMENTE ILUSTRATIVOS (TAIS COMO ELETROS, COLCHÕES, GRANITOS E DECORAÇÕES NO GERAL).

ASS: \_\_\_\_\_


**PRANCHA  
04**

## **VISÃO GERAL DOS MÓVEIS**


**VISTA A**

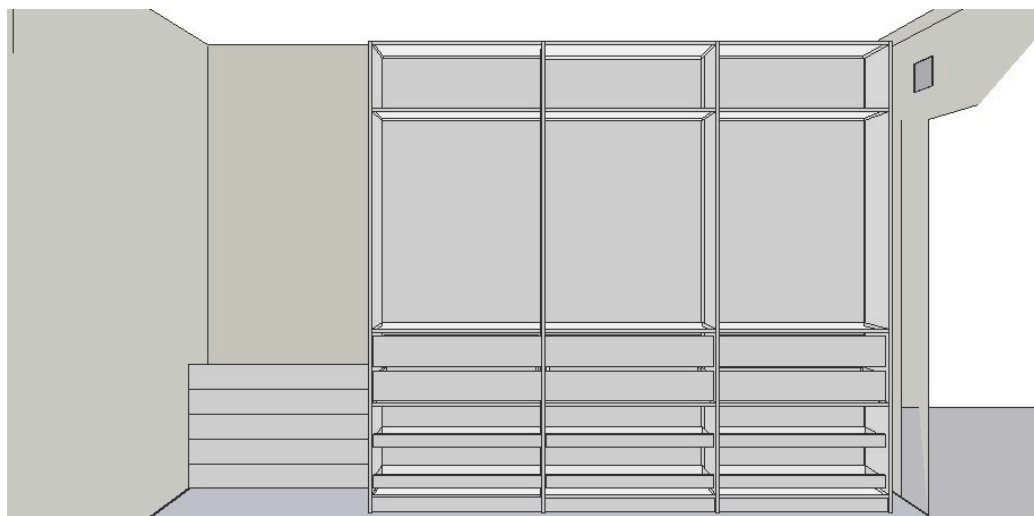


**VISTA B**

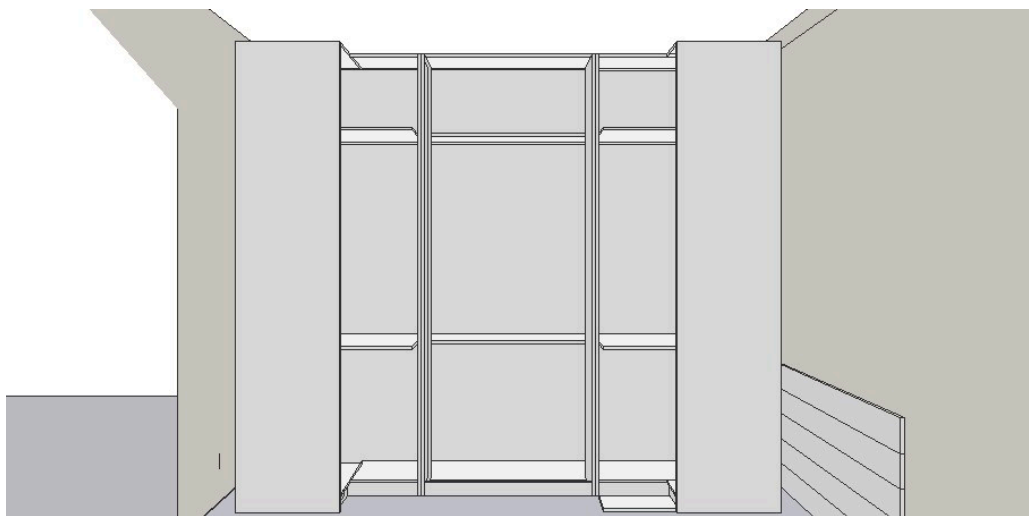

**VISTA C**

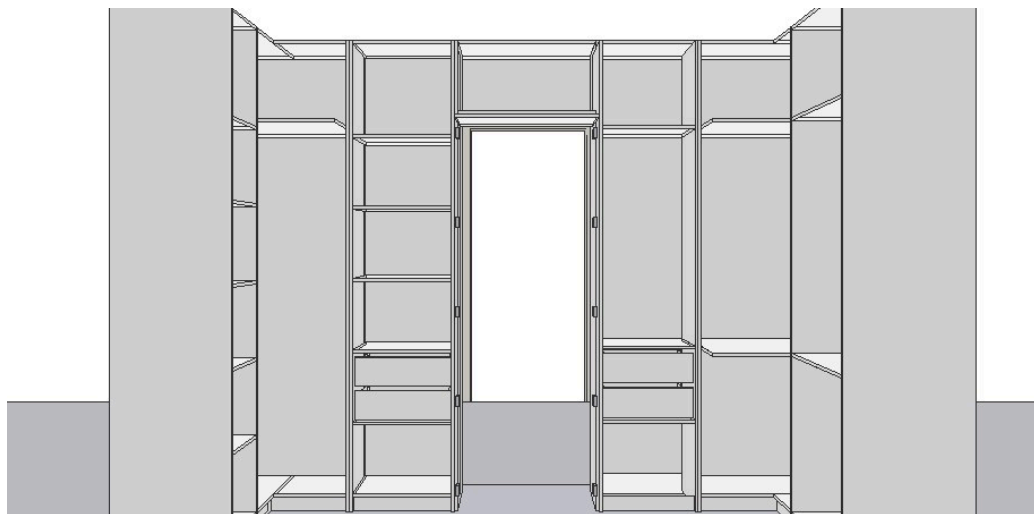

**VISTA D**

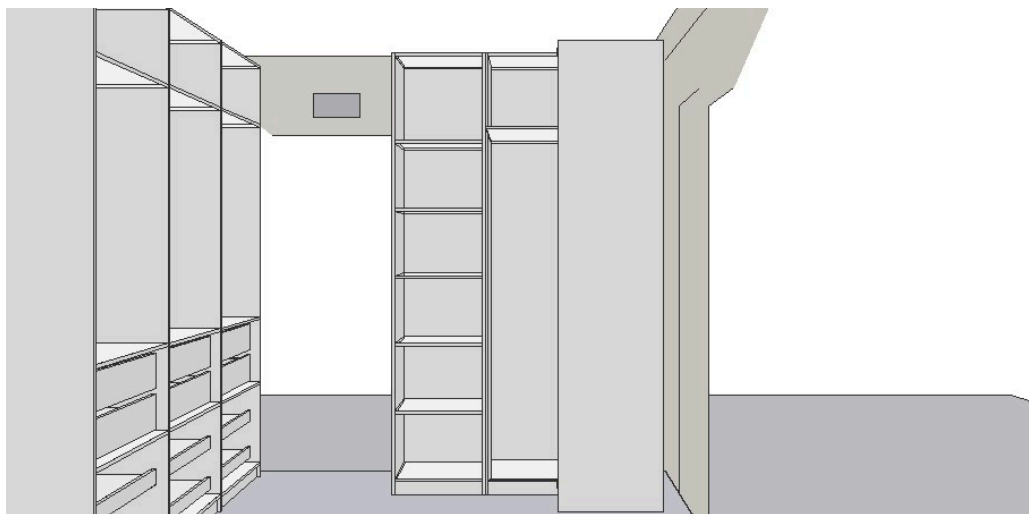



CLIENTE: **JAQUELINE DA SILVA**

AMBIENTE: **Closet**

PROJETISTA TÉCNICO: **JOÃO FELIPE SANTOS**

ARQUITETA: **FERNANDA**

**ATENÇÃO:**

DECLARO ESTAR DE ACORDO COM ESTE PROJETO E COM AS MEDIDAS NELE DESCRITAS E CIENTE DE QUE NELE CONSTAM APENAS PEÇAS E MÓDULOS DA EMPRESA, SENDO QUE OS DEMAIS ITENS SÃO MERAMENTE ILUSTRATIVOS (TAIS COMO ELETROS, COLCHÕES, GRANITOS E DECORAÇÕES NO GERAL).

ASS:.. \_\_\_\_\_

**PRANCHA  
05**

## MÓDULOS E PAINÉIS - VISTA A

| Item | Descrição                           | Dimensão      |
|------|-------------------------------------|---------------|
| 1    | Armário c/ Portas de Giro c/ Rodapé | 2902x2605x580 |
| 2    | Painel Branco MDP                   | 2700x18x150   |





CLIENTE: **JAQUELINE DA SILVA**

AMBIENTE: **Closet**

PROJETISTA TÉCNICO: **JOÃO FELIPE SANTOS**

ARQUITETA: **FERNANDA**


**ATENÇÃO:**

DECLARO ESTAR DE ACORDO COM ESTE PROJETO E COM AS MEDIDAS NELE DESCRITAS E CIENTE DE QUE NELE CONSTAM APENAS PEÇAS E MÓDULOS DA EMPRESA, SENDO QUE OS DEMAIS ITENS SÃO MERAMENTE ILUSTRATIVOS (TAIS COMO ELETROS, COLCHÕES, GRANITOS E DECORAÇÕES NO GERAL).

ASS:.. \_\_\_\_\_

**PRANCHA  
06**

**MEDIDAS E ALTURAS - VISTA A**

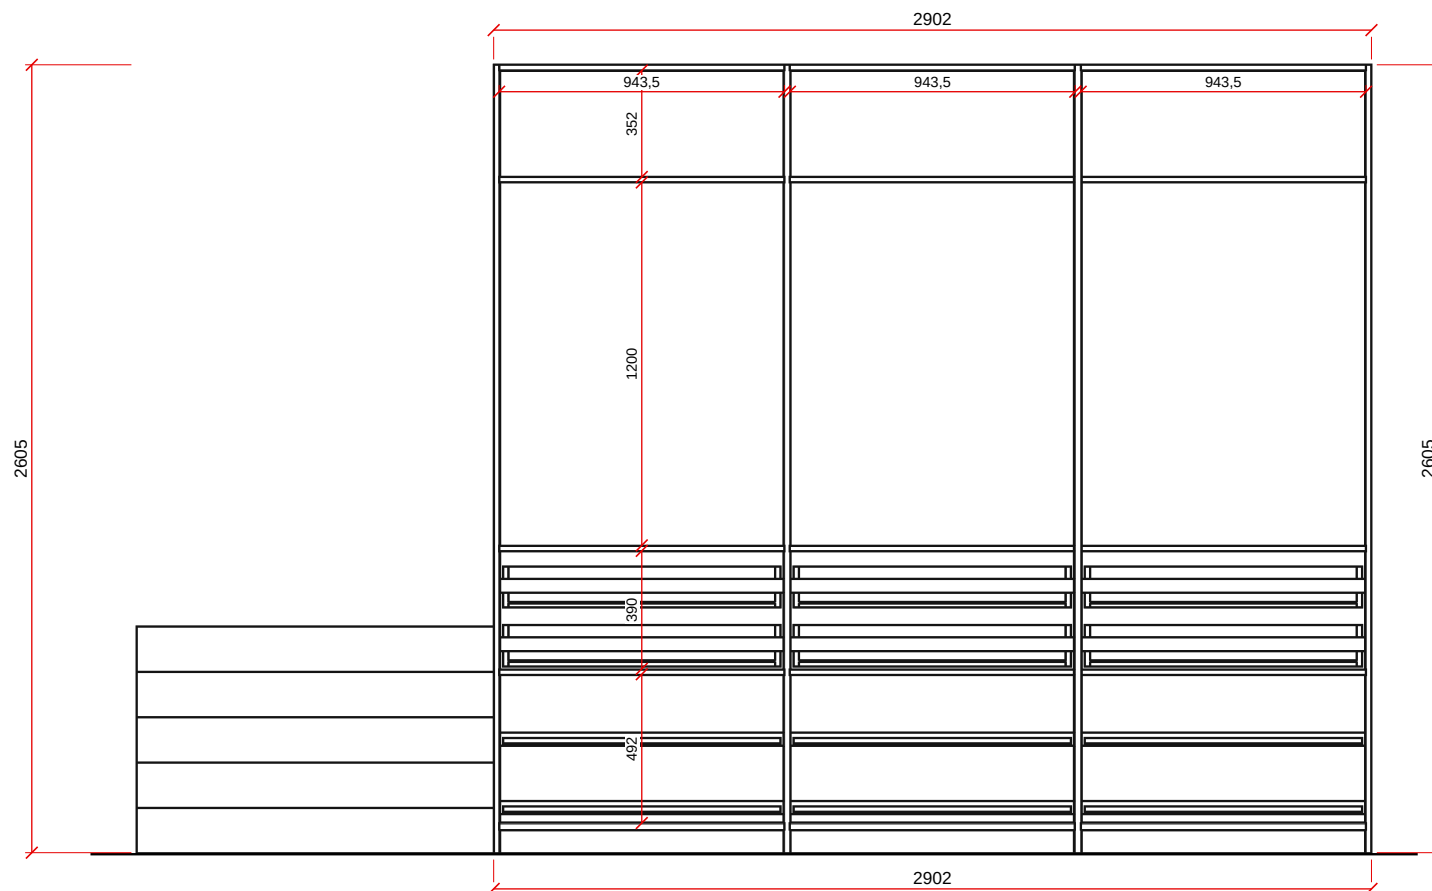

**VISTA A - ESC. 1:25**



CLIENTE: **JAQUELINE DA SILVA**

AMBIENTE: **Closet**

PROJETISTA TÉCNICO: **JOÃO FELIPE SANTOS**

ARQUITETA: **FERNANDA**

**ATENÇÃO:**

DECLARO ESTAR DE ACORDO COM ESTE PROJETO E COM AS MEDIDAS NELE DESCRITAS E CIENTE DE QUE NELE CONSTAM APENAS PEÇAS E MÓDULOS DA EMPRESA, SENDO QUE OS DEMAIS ITENS SÃO MERAMENTE ILUSTRATIVOS (TAIS COMO ELETROS, COLCHÕES, GRANITOS E DECORAÇÕES NO GERAL).


ASS.: \_\_\_\_\_

**PRANCHA  
07**



## MÓDULOS E PAINÉIS - VISTA B

| Item | Descrição                           | Dimensão       |
|------|-------------------------------------|----------------|
| 1    | Armário c/ Portas de Giro c/ Rodapé | 1026x2605x580  |
| 2    | Armário Canto L Esquerdo            | 1000x2605x1000 |

**Armário Canto L Esquerdo**

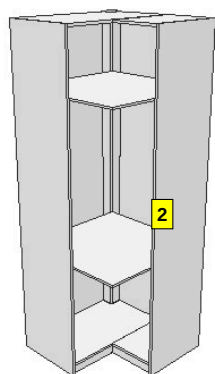

**Armário Canto L Esquerdo**

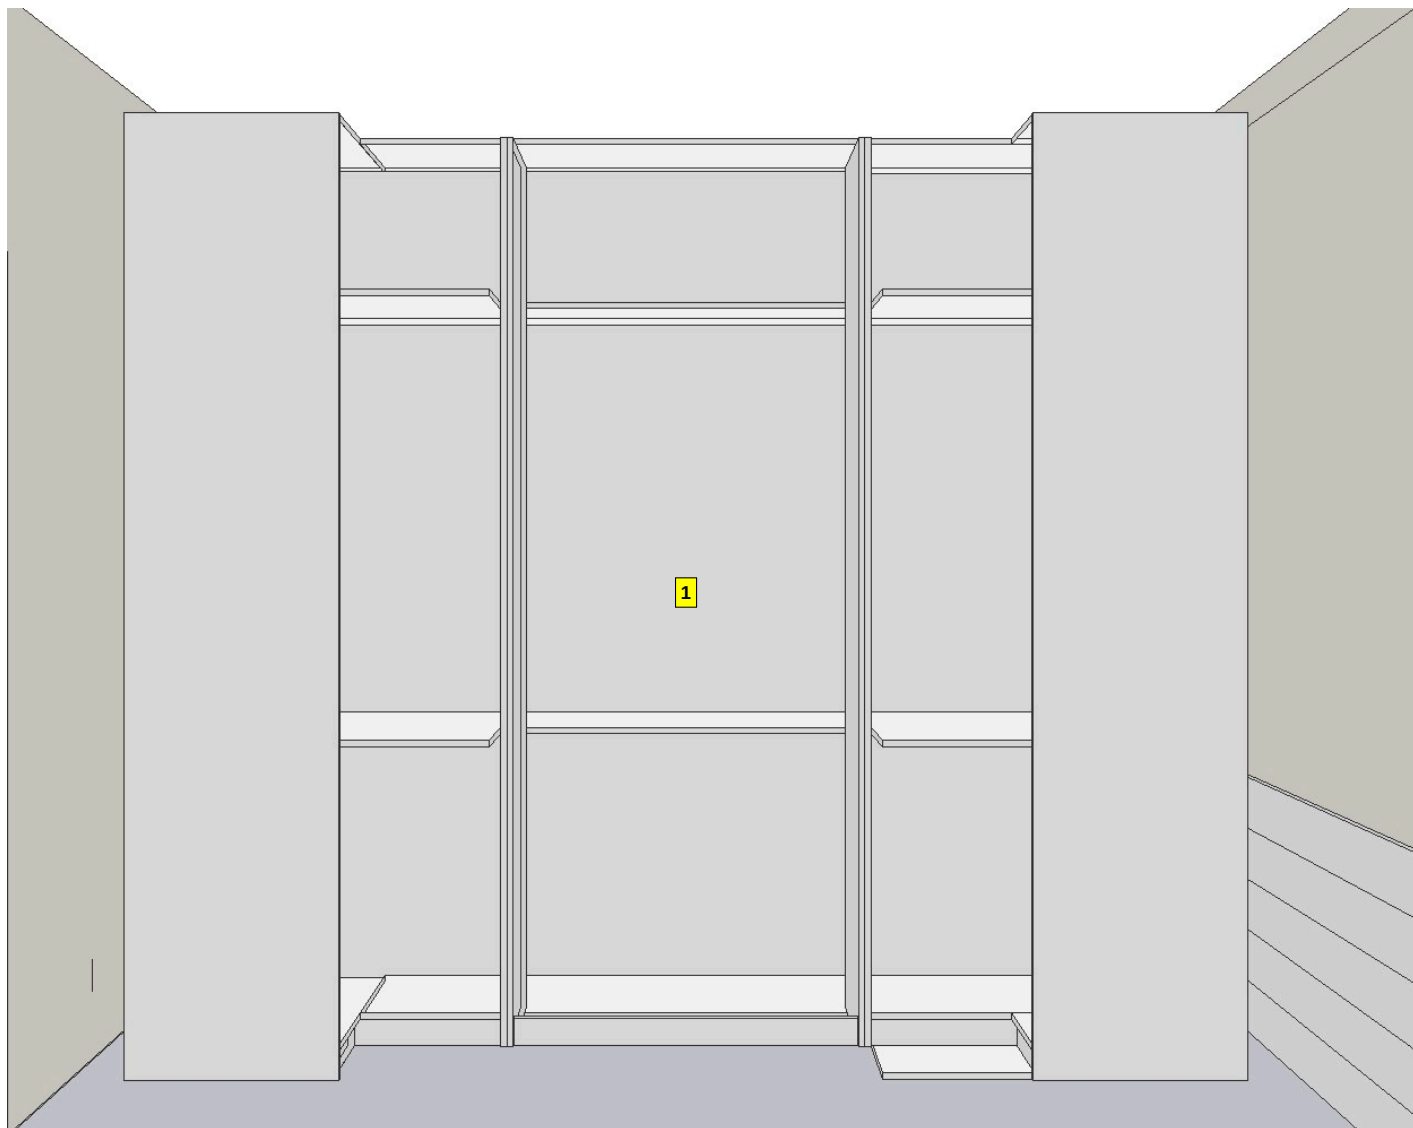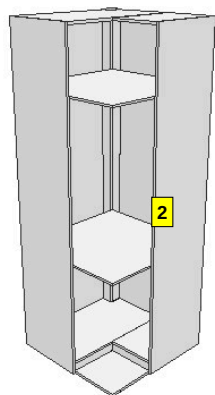



CLIENTE: **JAQUELINE DA SILVA**

AMBIENTE: **Closet**

PROJETISTA TÉCNICO: **JOÃO FELIPE SANTOS**

ARQUITETA: **FERNANDA**


**ATENÇÃO:**

DECLARO ESTAR DE ACORDO COM ESTE PROJETO E COM AS MEDIDAS NELE DESCRITAS E CIENTE DE QUE NELE CONSTAM APENAS PEÇAS E MÓDULOS DA EMPRESA, SENDO QUE OS DEMAIS ITENS SÃO MERAMENTE ILUSTRATIVOS (TAIS COMO ELETROS, COLCHÕES, GRANITOS E DECORAÇÕES NO GERAL).

ASS:.. \_\_\_\_\_

**PRANCHA  
08**

**MEDIDAS E ALTURAS - VISTA B**

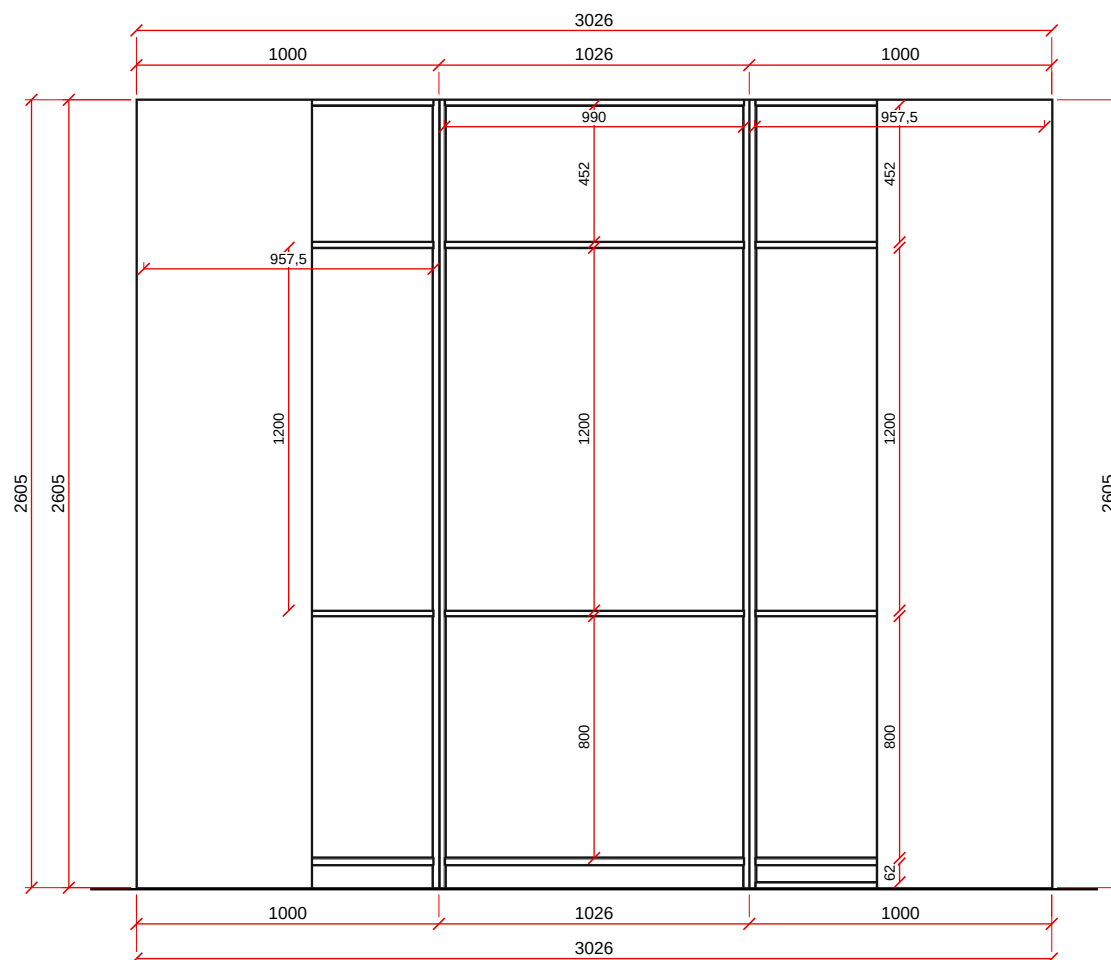

**VISTA B - ESC. 1:25**



CLIENTE: **JAQUELINE DA SILVA**

AMBIENTE: **Closet**

PROJETISTA TÉCNICO: **JOÃO FELIPE SANTOS**

ARQUITETA: **FERNANDA**

**ATENÇÃO:**

DECLARO ESTAR DE ACORDO COM ESTE PROJETO E COM AS MEDIDAS NELE DESCRITAS E CIENTE DE QUE NELE CONSTAM APENAS PEÇAS E MÓDULOS DA EMPRESA, SENDO QUE OS DEMAIS ITENS SÃO MERAMENTE ILUSTRATIVOS (TAIS COMO ELETROS, COLCHÕES, GRANITOS E DECORAÇÕES NO GERAL).



ASS.: \_\_\_\_\_

**PRANCHA  
09**

## MÓDULOS E PAINÉIS - VISTA C

| Item | Descrição                           | Dimensão     |
|------|-------------------------------------|--------------|
| 1    | Armário Superior                    | 802x405x580  |
| 2    | Armário c/ Portas de Giro c/ Rodapé | 550x2605x580 |
| 3    | Armário c/ Portas de Giro c/ Rodapé | 580x2605x580 |
| 4    | Painel Branco MDP                   | 802x18x560   |
| 5    | Painel Branco MDP                   | 2182x18x560  |

### DETALHE - NICHOS

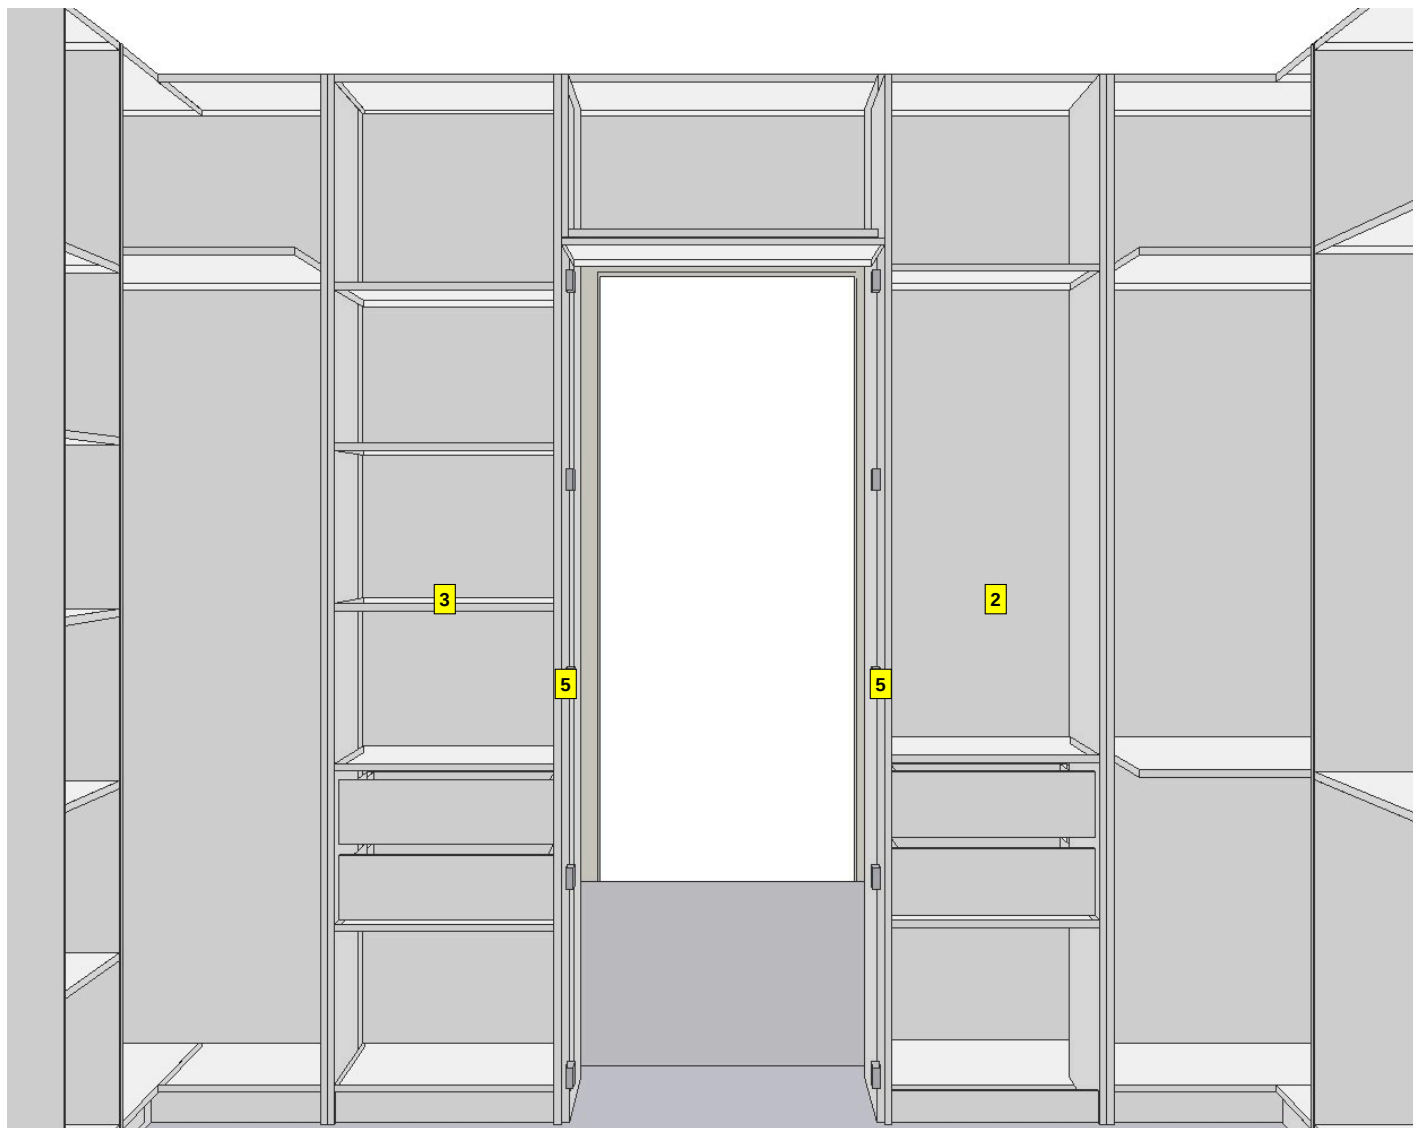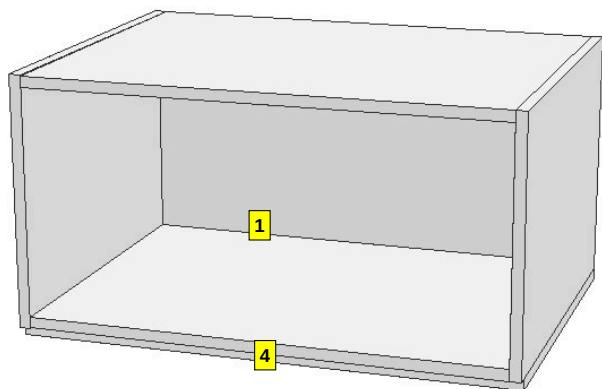



CLIENTE: **JAQUELINE DA SILVA**

AMBIENTE: **Closet**

PROJETISTA TÉCNICO: **JOÃO FELIPE SANTOS**

ARQUITETA: **FERNANDA**


**ATENÇÃO:**

DECLARO ESTAR DE ACORDO COM ESTE PROJETO E COM AS MEDIDAS NELE DESCRITAS E CIENTE DE QUE NELE CONSTAM APENAS PEÇAS E MÓDULOS DA EMPRESA, SENDO QUE OS DEMAIS ITENS SÃO MERAMENTE ILUSTRATIVOS (TAIS COMO ELETROS, COLCHÕES, GRANITOS E DECORAÇÕES NO GERAL).

ASS:.. \_\_\_\_\_

# PRANCHA 10

## MEDIDAS E ALTURAS - VISTA C

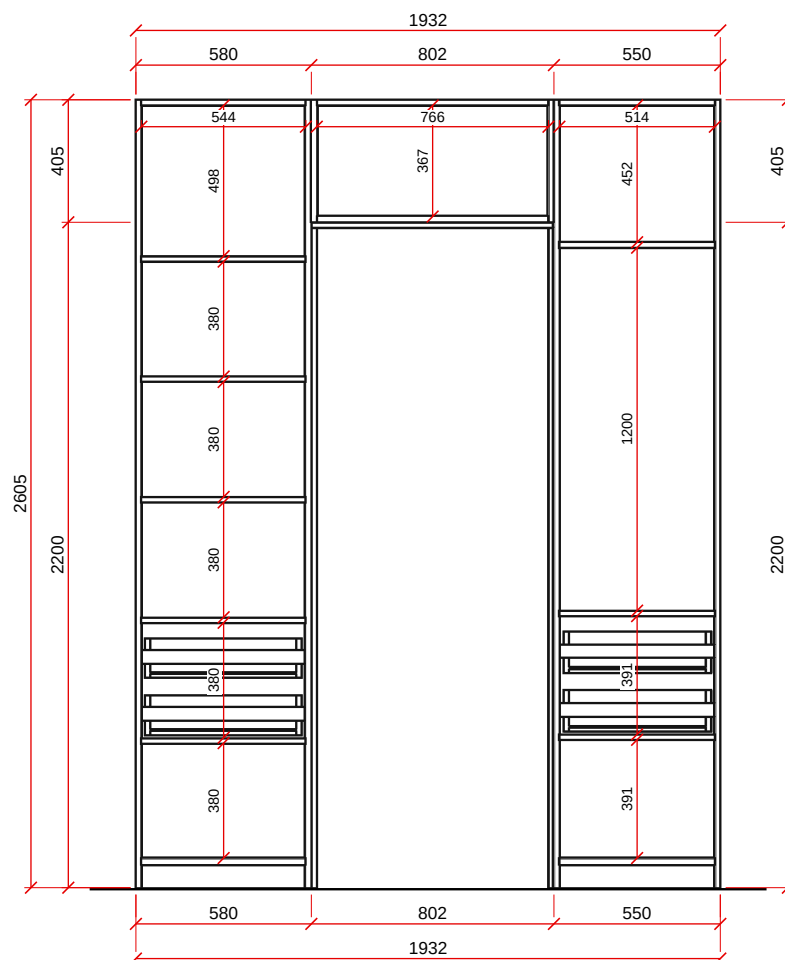

VISTA C - ESC. 1:25



CLIENTE: **JAQUELINE DA SILVA**

AMBIENTE: **Closet**

PROJETISTA TÉCNICO: **JOÃO FELIPE SANTOS**

ARQUITETA: **FERNANDA**

**ATENÇÃO:**

DECLARO ESTAR DE ACORDO COM ESTE PROJETO E COM AS MEDIDAS NELE DESCRITAS E CIENTE DE QUE NELE CONSTAM APENAS PEÇAS E MÓDULOS DA EMPRESA, SENDO QUE OS DEMAIS ITENS SÃO MERAMENTE ILUSTRATIVOS (TAIS COMO ELETROS, COLCHÕES, GRANITOS E DECORAÇÕES NO GERAL).



ASS.: \_\_\_\_\_

# PRANCHA 11

## MÓDULOS E PAINÉIS - VISTA D

| Item | Descrição                           | Dimensão       |
|------|-------------------------------------|----------------|
| 1    | Armário c/ Portas de Giro c/ Rodapé | 550x2605x580   |
| 2    | Armário Canto L Esquerdo            | 1000x2605x1000 |

**Armário Canto L Esquerdo**

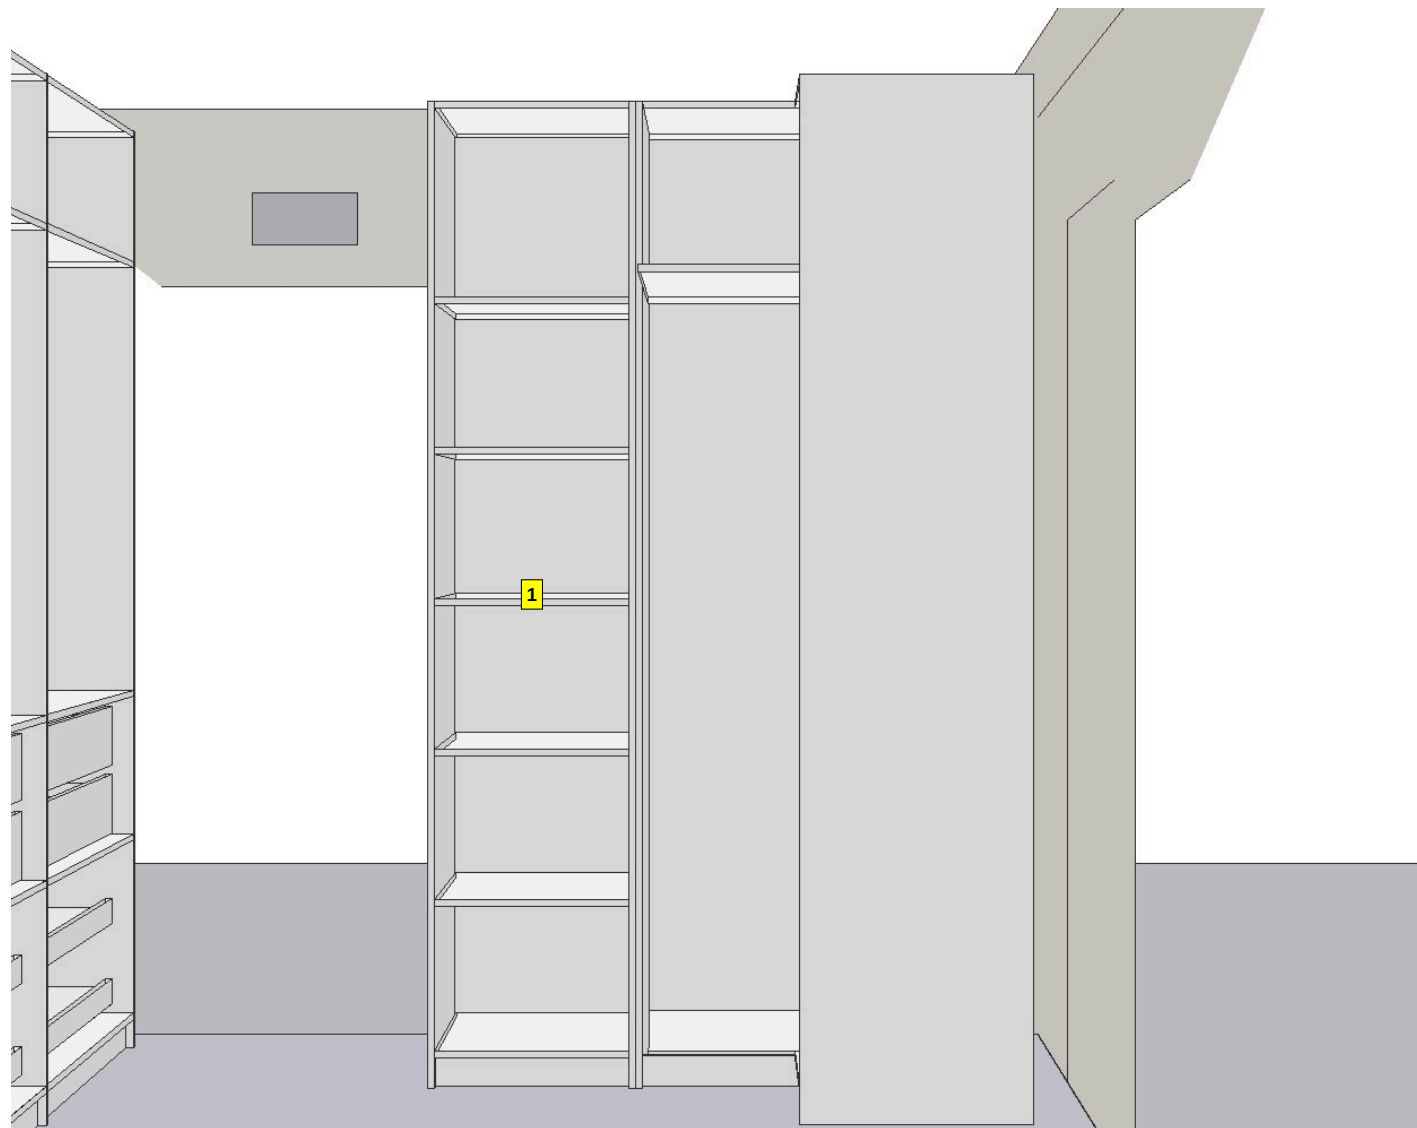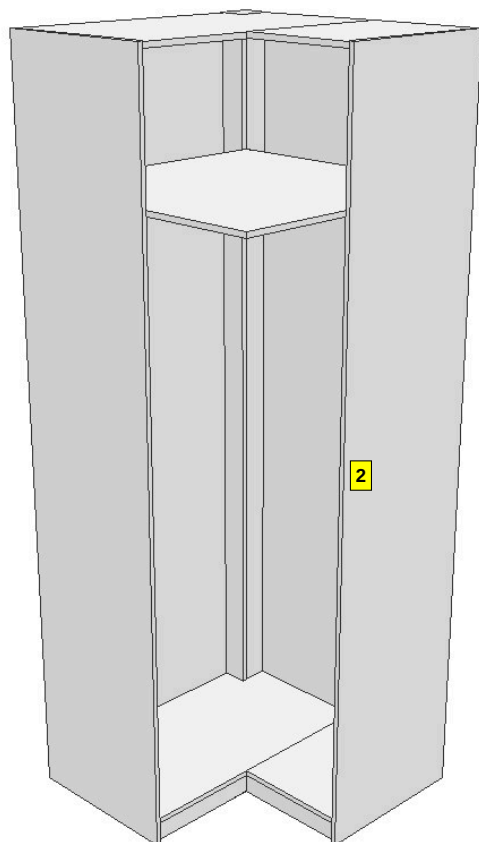



CLIENTE: **JAQUELINE DA SILVA**

AMBIENTE: **Closet**

PROJETISTA TÉCNICO: **JOÃO FELIPE SANTOS**

ARQUITETA: **FERNANDA**


**ATENÇÃO:**

DECLARO ESTAR DE ACORDO COM ESTE PROJETO E COM AS MEDIDAS NELE DESCRITAS E CIENTE DE QUE NELE CONSTAM APENAS PEÇAS E MÓDULOS DA EMPRESA, SENDO QUE OS DEMAIS ITENS SÃO MERAMENTE ILUSTRATIVOS (TAIS COMO ELETROS, COLCHÕES, GRANITOS E DECORAÇÕES NO GERAL).

ASS:.. \_\_\_\_\_

**PRANCHA  
12**

**MEDIDAS E ALTURAS - VISTA D**

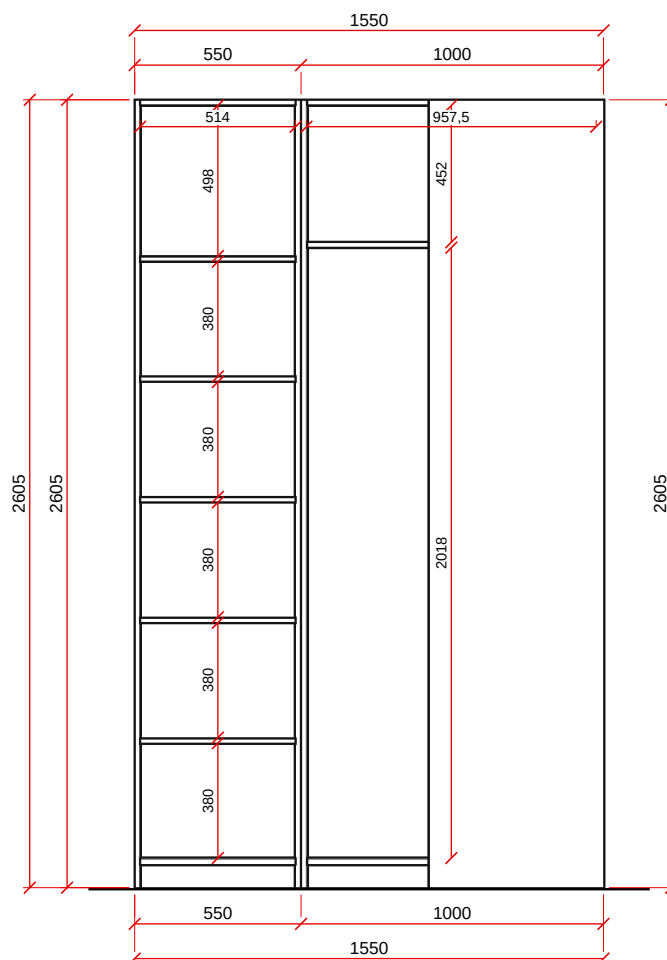

**VISTA D - ESC. 1:25**