



JAQUELINE DA SILVA

EXECUTIVO - COZINHA



CLIENTE: **JAQUELINE DA SILVA**

AMBIENTE: **Cozinha**

PROJETISTA TÉCNICO: **JOÃO FELIPE SANTOS**

ARQUITETA: **FERNANDA**

ATENÇÃO:

DECLARO ESTAR DE ACORDO COM ESTE PROJETO E COM AS MEDIDAS NELE DESCRITAS E CIENTE DE QUE NELE CONSTAM APENAS PEÇAS E MÓDULOS DA EMPRESA, SENDO QUE OS DEMAIS ITENS SÃO MERAMENTE ILUSTRATIVOS (TAIS COMO ELETROS, COLCHÕES, GRANITOS E DECORAÇÕES NO GERAL).

ASS: _____

**PRANCHA
02**

CONTRATO

LEIA COM ATENÇÃO

1- CLIENTE ESTÁ RECEBENDO UMA CÓPIA DOS PROJETOS ADQUIRIDOS E ESTÁ DE ACORDO COM AS INFORMAÇÕES APONTADAS SOBRE MODELO, COR, ACABAMENTO, ESTRUTURAS, ACESSÓRIOS E CONDIÇÕES QUE FAZEM PARTE DESTES PROJETOS EXECUTIVOS.

2- O MESMO FOI ELABORADO CONSIDERANDO AS MEDIDAS REAIS DESTES AMBIENTES, SE HOUVER ALGUMA ALTERAÇÃO NO PÉ DIREITO OU NAS PAREDES, REFERENTE À INSTALAÇÃO DE MOLDURAS DE GESSO, RODAPÉS, MODIFICAÇÃO EM INSTALAÇÃO DA MODULAÇÃO NO DIA DA MONTAGEM, A EMPRESA NÃO SE RESPONSABILIZA QUANTO A FUTUROS CONTRATEMPOS DEVIDOS ÀS ALTERAÇÕES. CABE AO CLIENTE AVISAR O PROJETISTA ANTES DA MEDIÇÃO FINAL PARA ADEQUAÇÃO DA MODULAÇÃO.

3- SE HOUVER GRANITO NOS AMBIENTES, A MEDIÇÃO FINAL SE DARÁ APÓS A CONCLUSÃO DA INSTALAÇÃO DOS MESMOS, OU INSTALAR APÓS A MONTAGEM DOS MÓVEIS.

4- SE HOUVER REDUÇÃO OU RECORTES NOS MÓDULOS, O CLIENTE TOMA CIÊNCIA QUE OS AJUSTES SERÃO EXECUTADOS NO LOCAL, QUE DEVE ESTAR LIVRE DE OBJETOS E PESSOAS QUE POSSAM SOFRER DE ALGUMA MANEIRA COM O PÓ DECORRENTE DESSES AJUSTES E QUALQUER OBJETO QUE NÃO POSSA SER RETIRADO DEVE ESTAR DEVIDAMENTE COBERTO. POR NÃO POSSUIR PROFISSIONÁIS ESPECIALIZADOS EM INSTALAÇÕES DE ELETROS, INSTALAÇÕES HIDRÁULICAS, A EMPRESA NÃO EFETUARÁ ESSE TIPO DE SERVIÇO. É NECESSÁRIO FORNECER AS PLANTAS DE INSTALAÇÃO ELÉTRICA E HIDRÁULICA DOS AMBIENTES NO DIA DA MONTAGEM, É NECESSÁRIO O ACOMPANHAMENTO DO CLIENTE OU UM RESPONSÁVEL PELA OBRA, MAIOR QUE 18 ANOS PARA TIRAR EVENTUAIS DÚVIDAS DOS MONTADORES REFERENTE AOS LOCAIS ONDE É POSSÍVEL FAZER FURAÇÕES. A ASSINATURA DESSE PROJETO SUBSTITUI QUALQUER PROJETO ANTERIOR.

5- O CLIENTE DECLARA ESTAR CIENTE QUE CASO O PROJETO ENVOLVA ELETROS, OS MESMOS DEVERÃO ESTAR NO LOCAL NO DIA DA MONTAGEM PARA ADEQUAÇÃO DOS NICHOS NECESSÁRIOS, E SE NÃO COMPROU OS ELETROS, SE RESPONSABILIZA EM ADQUIRIR OS MESMOS DENTRO DAS MEDIDAS ESPECIFICADAS NESTE PROJETO.

6- DECLARO ESTAR DE ACORDO COM ESTE PROJETO E COM AS MEDIDAS NELE DESCRITAS E CIENTE DE QUE NELE CONSTAM APENAS PEÇAS E MÓDULOS DA EMPRESA DUO PLANEJADOS, SENDO QUE OS DEMAIS ITENS SÃO MERAMENTE ILUSTRATIVOS (TAIS COMO ELETROS, COLCHÕES, GRANITOS E DECORAÇÕES EM GERAL).



CLIENTE: **JAQUELINE DA SILVA**

AMBIENTE: **Cozinha**

PROJETISTA TÉCNICO: **JOÃO FELIPE SANTOS**

ARQUITETA: **FERNANDA**

ATENÇÃO:

DECLARO ESTAR DE ACORDO COM ESTE PROJETO E COM AS MEDIDAS NELE DESCRITAS E CIENTE DE QUE NELE CONSTAM APENAS PEÇAS E MÓDULOS DA EMPRESA, SENDO QUE OS DEMAIS ITENS SÃO MERAMENTE ILUSTRATIVOS (TAIS COMO ELETROS, COLCHÕES, GRANITOS E DECORAÇÕES NO GERAL).

ASS.: _____

**PRANCHA
03**

PLANTA - ESPECIFICAÇÕES DO PROJETO

ESPECIFICAÇÕES DO PROJETO

CORES E ACABAMENTOS:

Caixa Módulos (Interno): **CONFERIR**

Portas e Frentes: **CONFERIR**

Tamponamentos: **CONFERIR**

Painéis e Tampas: **CONFERIR**

Puxadores: **CONFERIR**

Portas de Vidro: **CONFERIR**

FERRAGENS E ACESSÓRIOS:

Dobradiças: **CONFERIR**

Corrediças: **CONFERIR**

Puxadores: **CONFERIR**

Ferragens especiais: **CONFERIR**

ESPESSURAS:

Caixa Módulos (Interno): **18mm (fundo 6mm)**


Prateleiras internas: **18mm**

Portas e Frentes: **18mm**

Tamponamentos: **CONFERIR**

Painéis e Tampas e perfil: **18mm e 25mm**

1 item(ns) do XML não bateu(ram) com o DXF - conferir

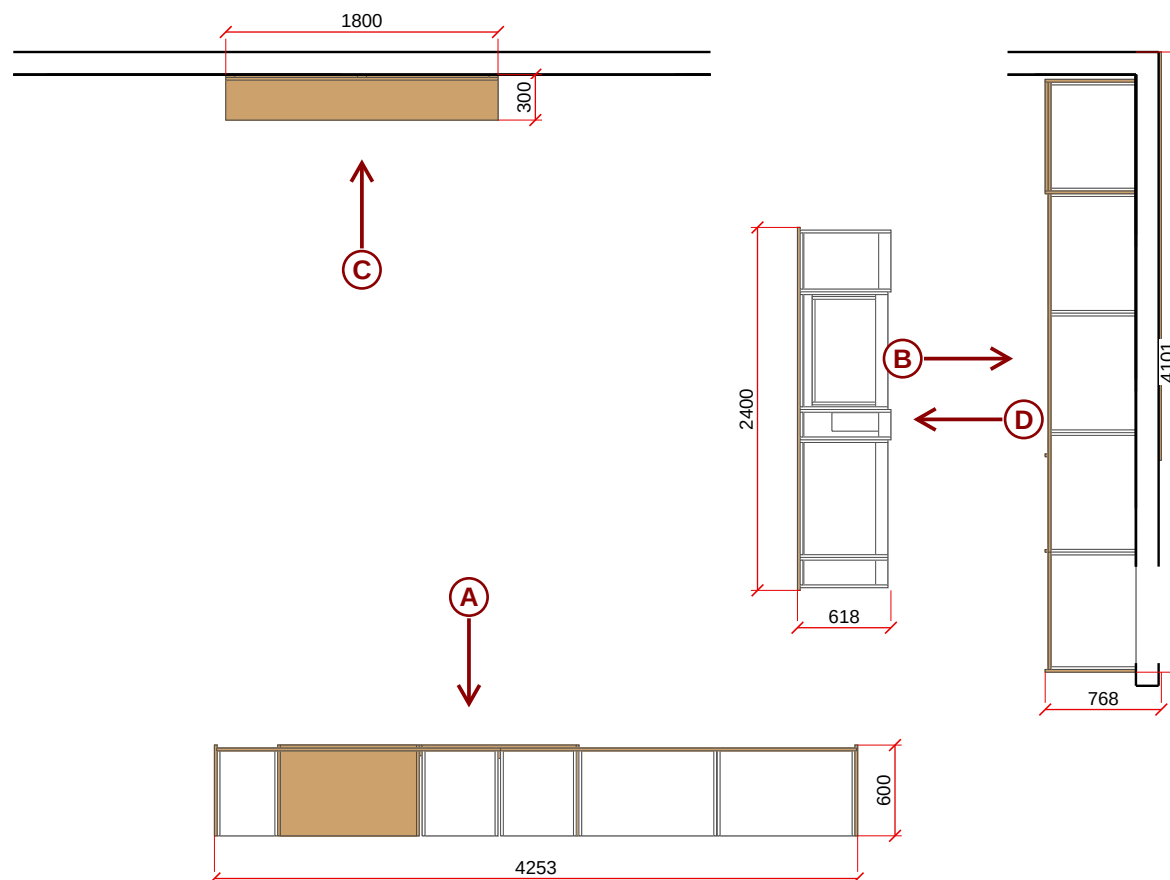

PLANTA BAIXA - ESC. 1:50



CLIENTE: **JAQUELINE DA SILVA**

AMBIENTE: **Cozinha**

PROJETISTA TÉCNICO: **JOÃO FELIPE SANTOS**

ARQUITETA: **FERNANDA**

ATENÇÃO:

DECLARO ESTAR DE ACORDO COM ESTE PROJETO E COM AS MEDIDAS NELE DESCRITAS E CIENTE DE QUE NELE CONSTAM APENAS PEÇAS E MÓDULOS DA EMPRESA, SENDO QUE OS DEMAIS ITENS SÃO MERAMENTE ILUSTRATIVOS (TAIS COMO ELETROS, COLCHÕES, GRANITOS E DECORAÇÕES NO GERAL).

ASS: _____

**PRANCHA
04**

VISÃO GERAL DOS MÓVEIS

VISTA A




VISTA B



VISTA C



VISTA D

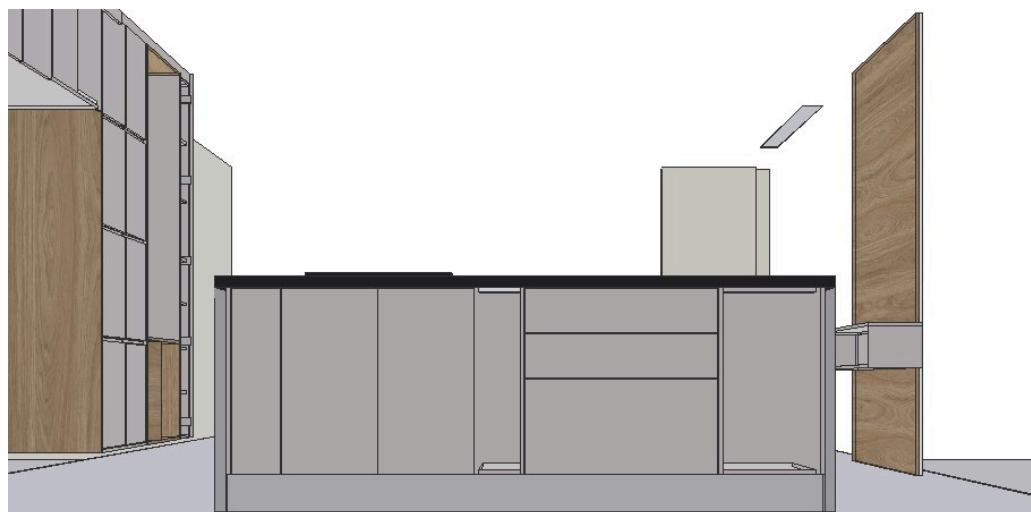



CLIENTE: **JAQUELINE DA SILVA**

AMBIENTE: **Cozinha**

PROJETISTA TÉCNICO: **JOÃO FELIPE SANTOS**

ARQUITETA: **FERNANDA**

ATENÇÃO:

DECLARO ESTAR DE ACORDO COM ESTE PROJETO E COM AS MEDIDAS NELE DESCRITAS E CIENTE DE QUE NELE CONSTAM APENAS PEÇAS E MÓDULOS DA EMPRESA, SENDO QUE OS DEMAIS ITENS SÃO MERAMENTE ILUSTRATIVOS (TAIS COMO ELETROS, COLCHÕES, GRANITOS E DECORAÇÕES NO GERAL).


ASS.: _____

**PRANCHA
05**

MÓDULOS E PAINÉIS - VISTA A - SUPERIORES

Item	Descrição	Dimensão
1	Armário Despenseiro	400x235x580
2	Armário Superior	500x570x580
3	Armário Superior	500x570x580
4	Armário Superior	500x570x580
5	Armário Superior	500x570x580
6	Armário Superior	910x537x580
7	Armário Superior	910x537x580
8	Painel Cinza Cristal MDF	1877x18x70
9	Painel Cinza Cristal MDF	500x18x70
10	Painel Cinza Cristal MDF	500x18x70
11	Painel Cinza Cristal MDF	500x18x70
12	Painel Cinza Cristal MDF	500x18x70
13	Painel Cinza Cristal MDF	2353x18x70
14	Painel Cinza Cristal MDF	2425x18x600
15	Painel Cinza Cristal MDF	2425x18x600
16	Painel Cinza Cristal MDF	2355x18x70
17	Painel Cinza Cristal MDF	2355x18x600
18	Painel Cinza Cristal MDF	1820x18x580
19	Painel Itapua MDF	862x18x900
20	Painel Itapua MDF	900x18x600
21	Painel Itapua MDF	2355x18x600
22	Painel Itapua MDF	2355x18x600
23	Painel Itapua MDF	900x25x300
24	Painel Itapua MDF	2335x18x70

DETALHE - PORTA AUSENTE

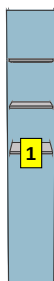



CLIENTE: **JAQUELINE DA SILVA**

AMBIENTE: **Cozinha**

PROJETISTA TÉCNICO: **JOÃO FELIPE SANTOS**

ARQUITETA: **FERNANDA**

ATENÇÃO:

DECLARO ESTAR DE ACORDO COM ESTE PROJETO E COM AS MEDIDAS NELE DESCRITAS E CIENTE DE QUE NELE CONSTAM APENAS PEÇAS E MÓDULOS DA EMPRESA, SENDO QUE OS DEMAIS ITENS SÃO MERAMENTE ILUSTRATIVOS (TAIS COMO ELETROS, COLCHÕES, GRANITOS E DECORAÇÕES NO GERAL).

ASS.: _____

**PRANCHA
06**

MÓDULOS E PAINÉIS - VISTA A - INFERIORES

Item	Descrição	Dimensão
1	Armário Superior	500x570x580
2	Armário Superior	500x570x580
3	Armário Superior	500x570x580
4	Armário Superior	500x570x580
5	Balcão Inferior	525x600x580
6	Painel Cinza Cristal MDF	500x18x70
7	Painel Cinza Cristal MDF	500x18x70
8	Painel Cinza Cristal MDF	1020x18x70
9	Painel Itapua MDF	600x18x357
10	Painel Itapua MDF	600x18x600
11	Painel Itapua MDF	900x18x600
12	Painel Itapua MDF	900x18x600
13	Painel Itapua MDF	814x18x900





CLIENTE: **JAQUELINE DA SILVA**

AMBIENTE: **Cozinha**

PROJETISTA TÉCNICO: **JOÃO FELIPE SANTOS**

ARQUITETA: **FERNANDA**

ATENÇÃO:

DECLARO ESTAR DE ACORDO COM ESTE PROJETO E COM AS MEDIDAS NELE DESCRITAS E CIENTE DE QUE NELE CONSTAM APENAS PEÇAS E MÓDULOS DA EMPRESA, SENDO QUE OS DEMAIS ITENS SÃO MERAMENTE ILUSTRATIVOS (TAIS COMO ELETROS, COLCHÕES, GRANITOS E DECORAÇÕES NO GERAL).

ASS: _____

**PRANCHA
08**

MÓDULOS E PAINÉIS - VISTA B - SUPERIORES

Item	Descrição	Dimensão
1	Armário Superior	720x701x580
2	Armário Superior	776x387x580
3	Armário Superior	778x330x350
4	Armário Superior	778x330x350
5	Armário Superior	779x330x350
6	Armário Superior	790x567x580
7	Armário Superior	790x567x580
8	Armário Superior	790x567x580
9	Painel Cinza Cristal MDF	2334x18x70
10	Painel Cinza Cristal MDF	2425x18x600
11	Painel Cinza Cristal MDF	2425x18x600
12	Painel Cinza Cristal MDF	739x25x100
13	Painel Cinza Cristal MDF	776x18x70
14	Painel Cinza Cristal MDF	2370x18x580
15	Painel Cinza Cristal MDF	2370x18x70
16	Painel Cinza Cristal MDF	720x18x70
17	Painel Cinza Cristal MDF	2550x18x600
18	Painel Itapua MDF	2337x18x350





CLIENTE: **JAQUELINE DA SILVA**

AMBIENTE: **Cozinha**

PROJETISTA TÉCNICO: **JOÃO FELIPE SANTOS**

ARQUITETA: **FERNANDA**

ATENÇÃO:


DECLARO ESTAR DE ACORDO COM ESTE PROJETO E COM AS MEDIDAS NELE DESCRITAS E CIENTE DE QUE NELE CONSTAM APENAS PEÇAS E MÓDULOS DA EMPRESA, SENDO QUE OS DEMAIS ITENS SÃO MERAMENTE ILUSTRATIVOS (TAIS COMO ELETROS, COLCHÕES, GRANITOS E DECORAÇÕES NO GERAL).

ASS.: _____

**PRANCHA
09**

MÓDULOS E PAINÉIS - VISTA B - INFERIORES

Item	Descrição	Dimensão
1	Balcão Inferior	400x750x580
2	Balcão Inferior	400x750x580
3	Balcão Inferior	720x400x580
4	Balcão Inferior	920x750x580
5	Painel Cinza Cristal MDF	750x18x600
6	Painel Cinza Cristal MDF	750x18x600
7	Painel Cinza Cristal MDF	1254x18x720
8	Painel Cinza Cristal MDF	2075x18x580

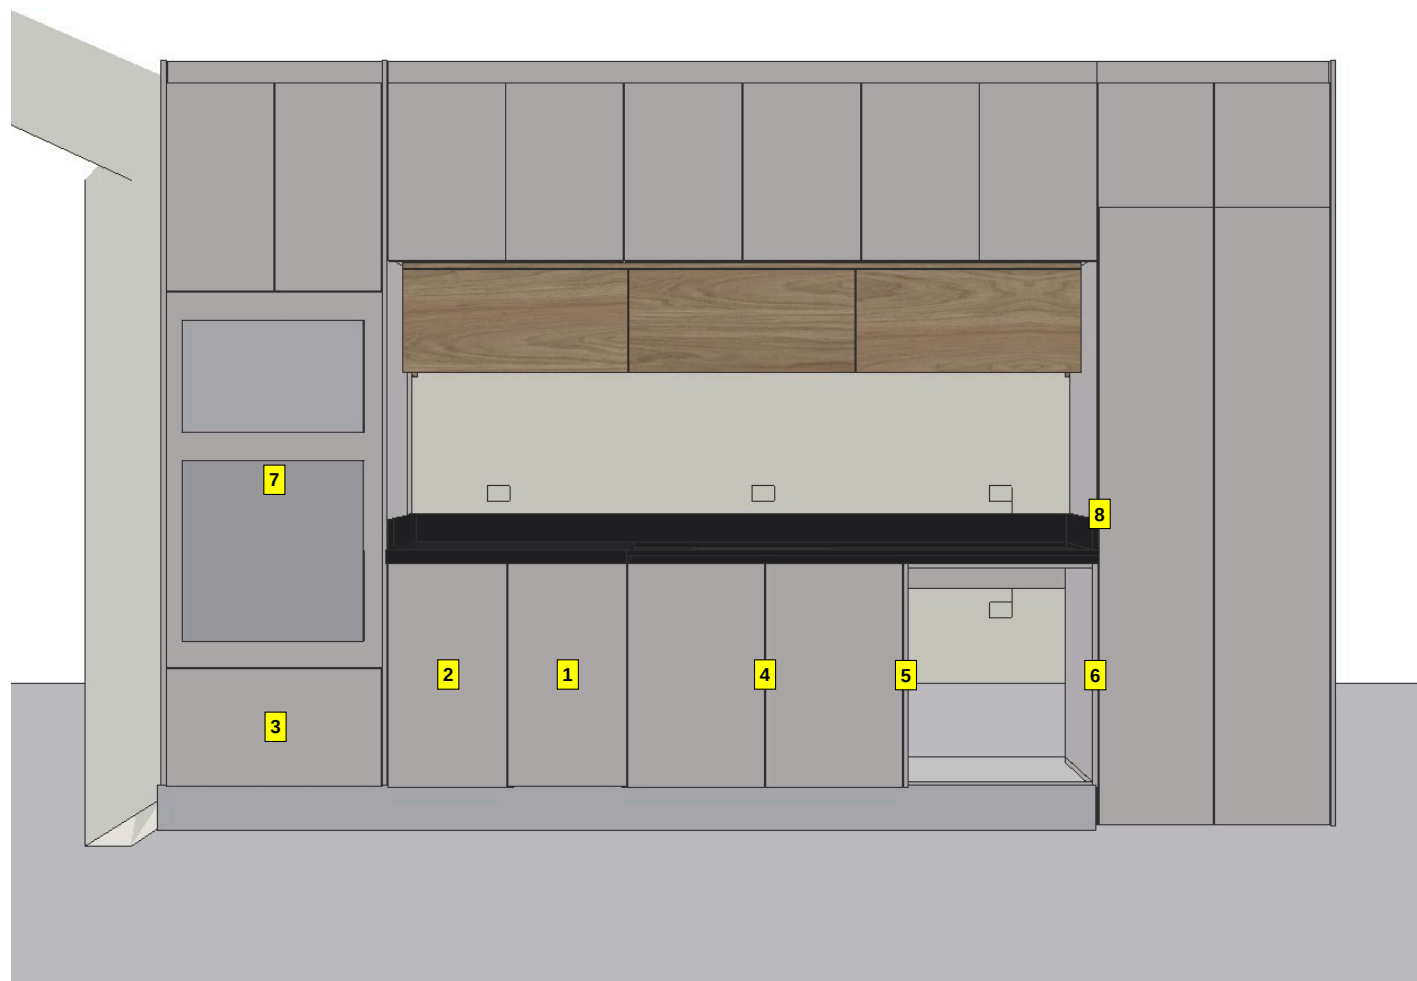



CLIENTE: **JAQUELINE DA SILVA**

AMBIENTE: **Cozinha**

PROJETISTA TÉCNICO: **JOÃO FELIPE SANTOS**

ARQUITETA: **FERNANDA**


ATENÇÃO:

DECLARO ESTAR DE ACORDO COM ESTE PROJETO E COM AS MEDIDAS NELE DESCRITAS E CIENTE DE QUE NELE CONSTAM APENAS PEÇAS E MÓDULOS DA EMPRESA, SENDO QUE OS DEMAIS ITENS SÃO MERAMENTE ILUSTRATIVOS (TAIS COMO ELETROS, COLCHÕES, GRANITOS E DECORAÇÕES NO GERAL).

ASS.: _____

PRANCHA 10

MEDIDAS E ALTURAS - VISTA B

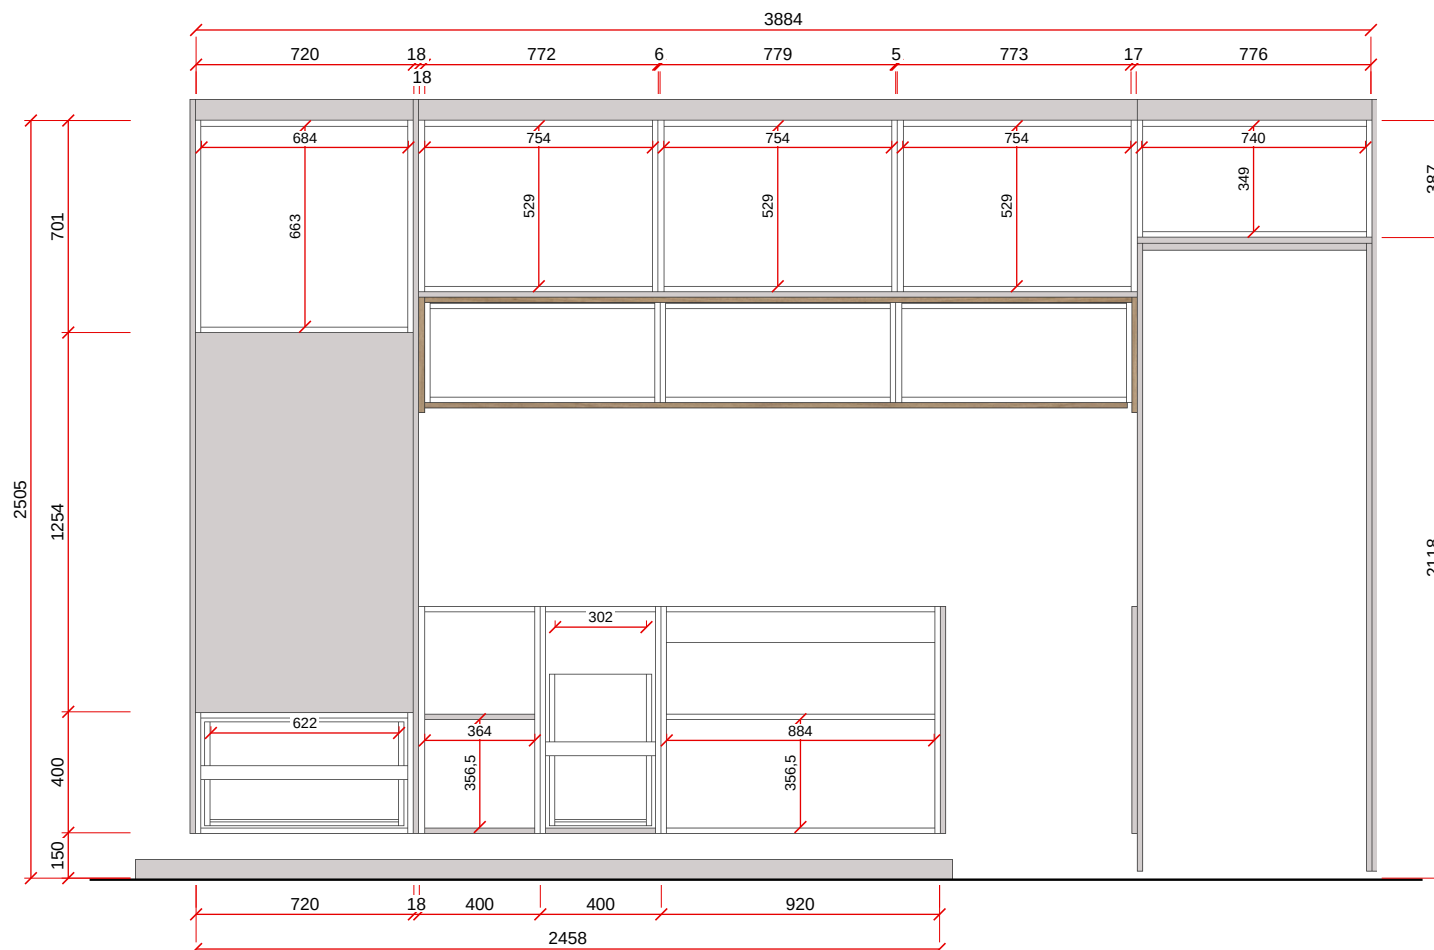

VISTA B - ESC. 1:25



CLIENTE: **JAQUELINE DA SILVA**

AMBIENTE: **Cozinha**

PROJETISTA TÉCNICO: **JOÃO FELIPE SANTOS**

ARQUITETA: **FERNANDA**

ATENÇÃO:


DECLARO ESTAR DE ACORDO COM ESTE PROJETO E COM AS MEDIDAS NELE DESCRITAS E CIENTE DE QUE NELE CONSTAM APENAS PEÇAS E MÓDULOS DA EMPRESA, SENDO QUE OS DEMAIS ITENS SÃO MERAMENTE ILUSTRATIVOS (TAIS COMO ELETROS, COLCHÕES, GRANITOS E DECORAÇÕES NO GERAL).

ASS.: _____

PRANCHA 11

MÓDULOS E PAINÉIS - VISTA C

Item	Descrição	Dimensão
1	Painel Cinza Cristal MDF	232x18x300
2	Painel Cinza Cristal MDF	1764x18x300
3	Painel Cinza Cristal MDF	1800x18x300
4	Painel Cinza Cristal MDF	214x18x1764
5	Painel Itapua MDF	1725x18x1800
6	Painel Itapua MDF	600x18x1800

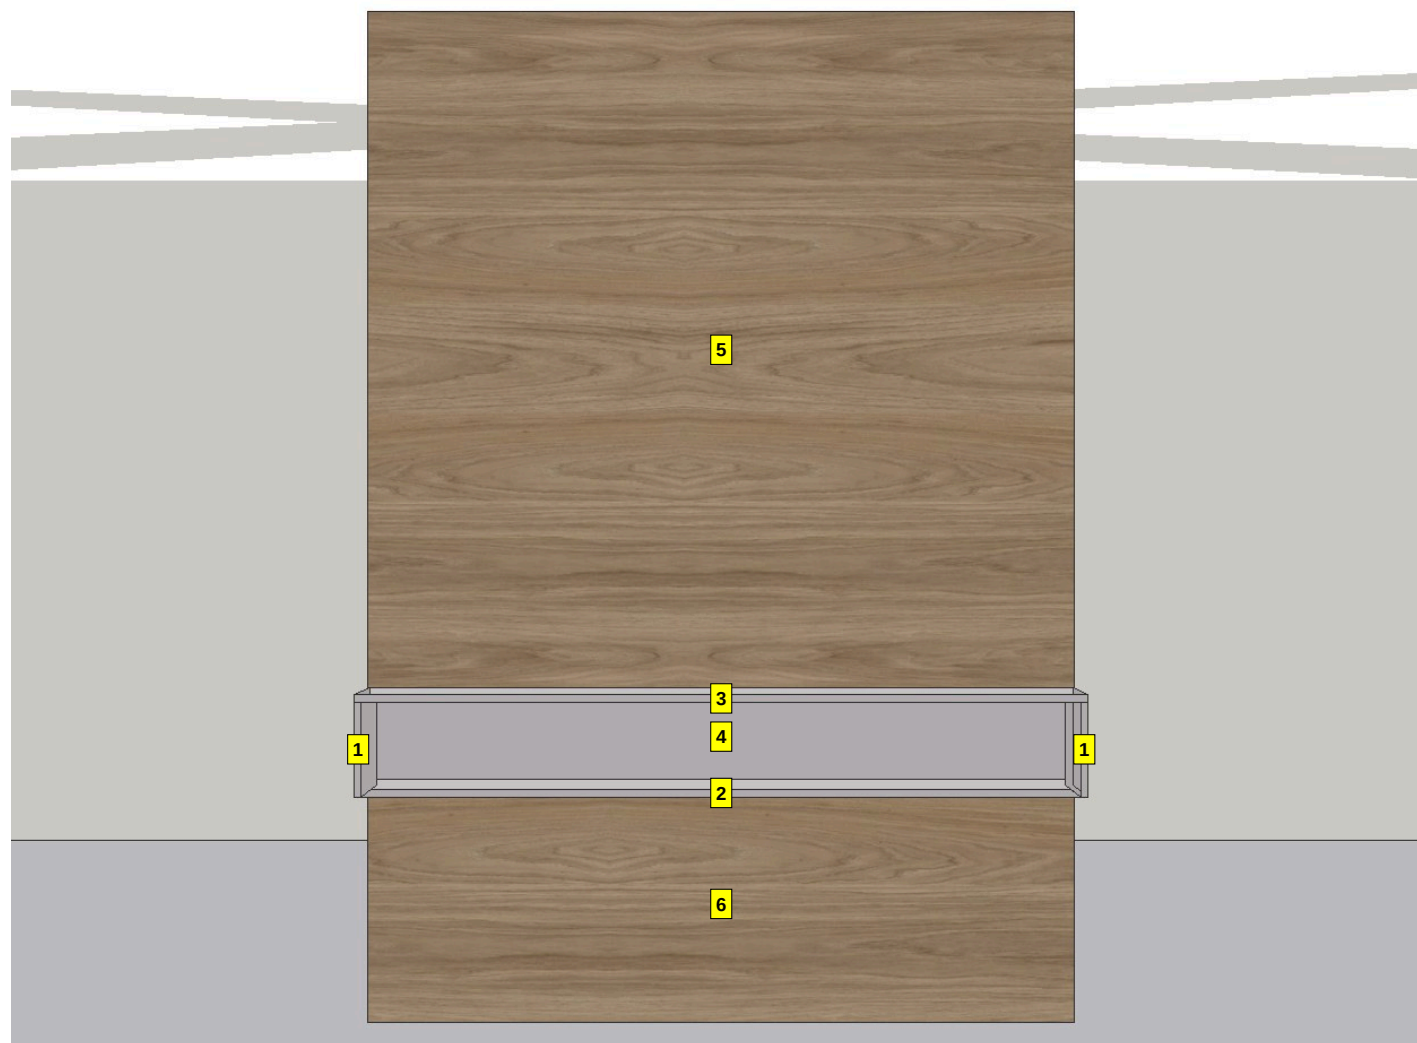



CLIENTE: **JAQUELINE DA SILVA**

AMBIENTE: **Cozinha**

PROJETISTA TÉCNICO: **JOÃO FELIPE SANTOS**

ARQUITETA: **FERNANDA**

ATENÇÃO:

DECLARO ESTAR DE ACORDO COM ESTE PROJETO E COM AS MEDIDAS NELE DESCRITAS E CIENTE DE QUE NELE CONSTAM APENAS PEÇAS E MÓDULOS DA EMPRESA, SENDO QUE OS DEMAIS ITENS SÃO MERAMENTE ILUSTRATIVOS (TAIS COMO ELETROS, COLCHÕES, GRANITOS E DECORAÇÕES NO GERAL).

ASS:.. _____

PRANCHA 12

MEDIDAS E ALTURAS - VISTA C



VISTA C - ESC. 1:25



CLIENTE: **JAQUELINE DA SILVA**

AMBIENTE: **Cozinha**

PROJETISTA TÉCNICO: **JOÃO FELIPE SANTOS**

ARQUITETA: **FERNANDA**

ATENÇÃO:

DECLARO ESTAR DE ACORDO COM ESTE PROJETO E COM AS MEDIDAS NELE DESCRITAS E CIENTE DE QUE NELE CONSTAM APENAS PEÇAS E MÓDULOS DA EMPRESA, SENDO QUE OS DEMAIS ITENS SÃO MERAMENTE ILUSTRATIVOS (TAIS COMO ELETROS, COLCHÕES, GRANITOS E DECORAÇÕES NO GERAL).


ASS.: _____

PRANCHA 13



MÓDULOS E PAINÉIS - VISTA D

Item	Descrição	Dimensão
1	Balcão Inferior	200x750x580
2	Balcão Inferior	200x750x600
3	Balcão Inferior	408x750x600
4	Balcão Inferior	778x750x580

DETALHE - PORTA AUSENTE

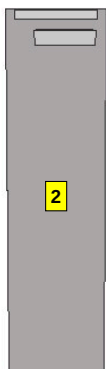

DETALHE - PORTA AUSENTE

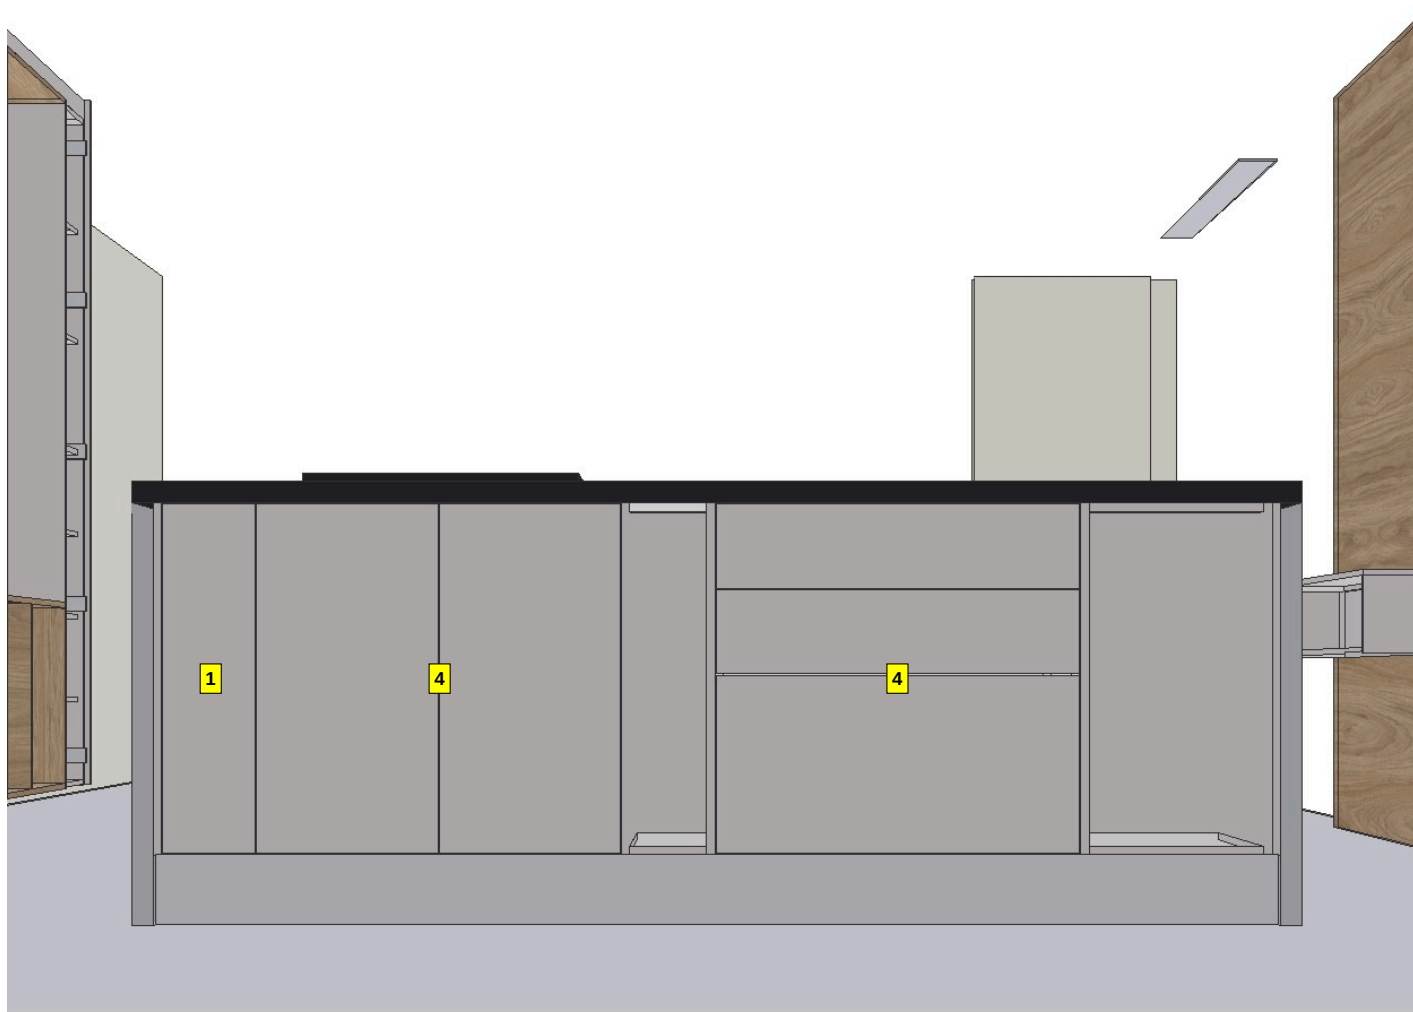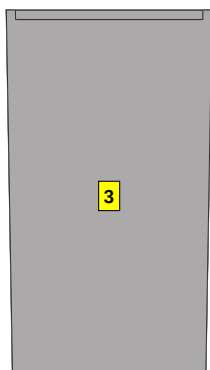

VISTA D - ESC. 1:12.5